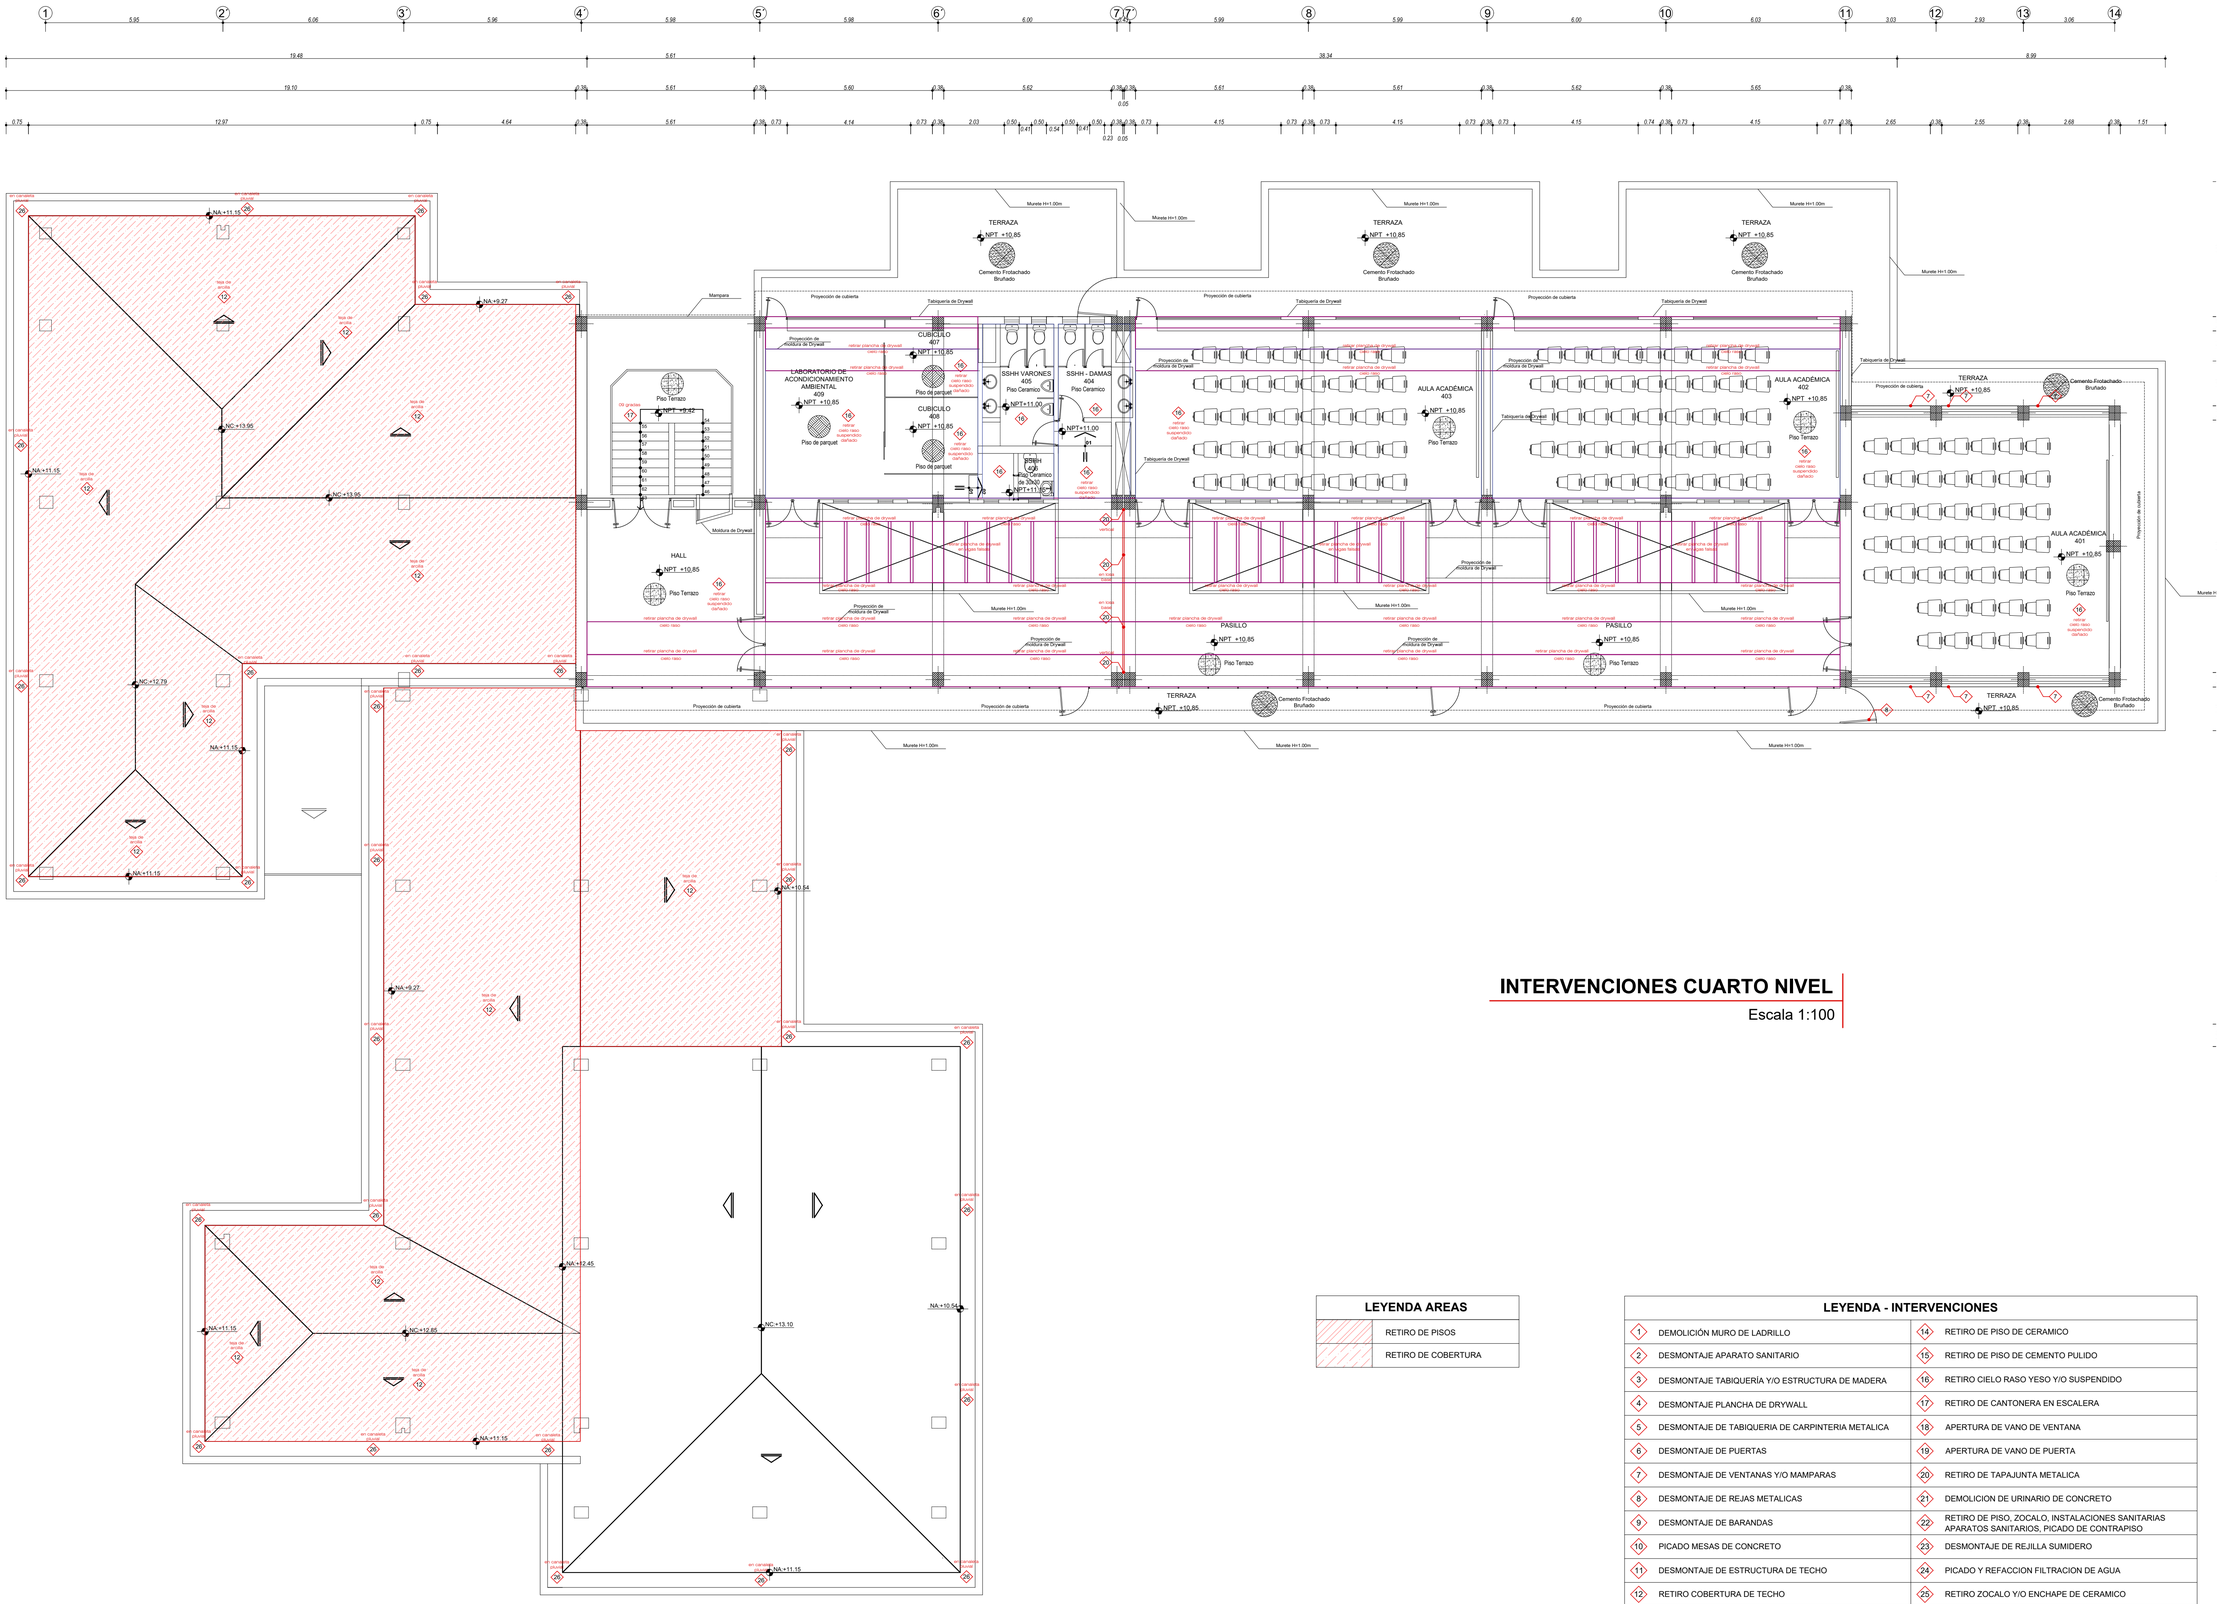

INTERVENCIONES CUARTO NIVEL

Escala 1:100

LEYENDA AREAS	
	RETIRO DE PISOS
	RETIRO DE COBERTURA

LEYENDA - INTERVENCIONES			
1	DEMOLICIÓN MURO DE LADRILLO	14	RETIRO DE PISO DE CERAMICO
2	DESMONTAJE APARATO SANITARIO	15	RETIRO DE PISO DE CEMENTO PULIDO
3	DESMONTAJE TABIQUERÍA Y/O ESTRUCTURA DE MADERA	16	RETIRO CIELO RASO YESO Y/O SUSPENDIDO
4	DESMONTAJE PLANCHA DE DRYWALL	17	RETIRO DE CANTONERA EN ESCALERA
5	DESMONTAJE DE TABIQUERIA DE CARPINTERIA METALICA	18	APERTURA DE VANO DE VENTANA
6	DESMONTAJE DE PUERTAS	19	APERTURA DE VANO DE PUERTA
7	DESMONTAJE DE VENTANAS Y/O MAMPARAS	20	RETIRO DE TAPAJUNTA METALICA
8	DESMONTAJE DE REJAS METALICAS	21	DEMOLICION DE URINARIO DE CONCRETO
9	DESMONTAJE DE BARANDAS	22	RETIRO DE PISO, ZOCALO, INSTALACIONES SANITARIAS APARATOS SANITARIOS, PICADO DE CONTRAPISO
10	PICADO MESAS DE CONCRETO	23	DESMONTAJE DE REJILLA SUMIDERO
11	DESMONTAJE DE ESTRUCTURA DE TECHO	24	PICADO Y REFACCION FILTRACION DE AGUA
12	RETIRO COBERTURA DE TECHO	25	RETIRO ZOCALO Y/O ENCHAPE DE CERAMICO
13	RETIRO DE PISO DE PARQUET	26	PICADO TARRAJEO EXISTENTE

ENTIDAD:

UNIVERSIDAD NACIONAL DE SAN ANTONIO ABAD DEL CUSCO

PROYECTO:

"SERVICIO DE CONSULTORIA PARA LA ELABORACION DEL EXPEDIENTE DE REHABILITACION Y DIAGNOSTICO CON FINES DE LICENCIAMIENTO DE LA INFRAESTRUCTURA DE LA UNIVERSIDAD NACIONAL DE SAN ANTONIO ABAD DEL CUSCO" - ITEM 4

REGION: CUSCO

DEPARTAMENTO: CUSCO

PROVINCIA: CUSCO

DISTRITO: CUSCO

LOCALIDAD: PERAYOC

FACULTAD: ARQUITECTURA E INGENIERÍA CIVIL

ESCUELA PROFESIONAL: ARQUITECTURA

LUGAR: PABELLON ESCUELA PROFESIONAL DE ARQUITECTURA

CONSULTOR:

CONSORCIO ROJAS SOTO

EXPEDIENTE:

REHABILITACION

PLANO:

INTERVENCIONES
NIVEL 4

DIBUJO:

ESCALA: INDICADA

FECHA: NOVIEMBRE 2017

AI.04