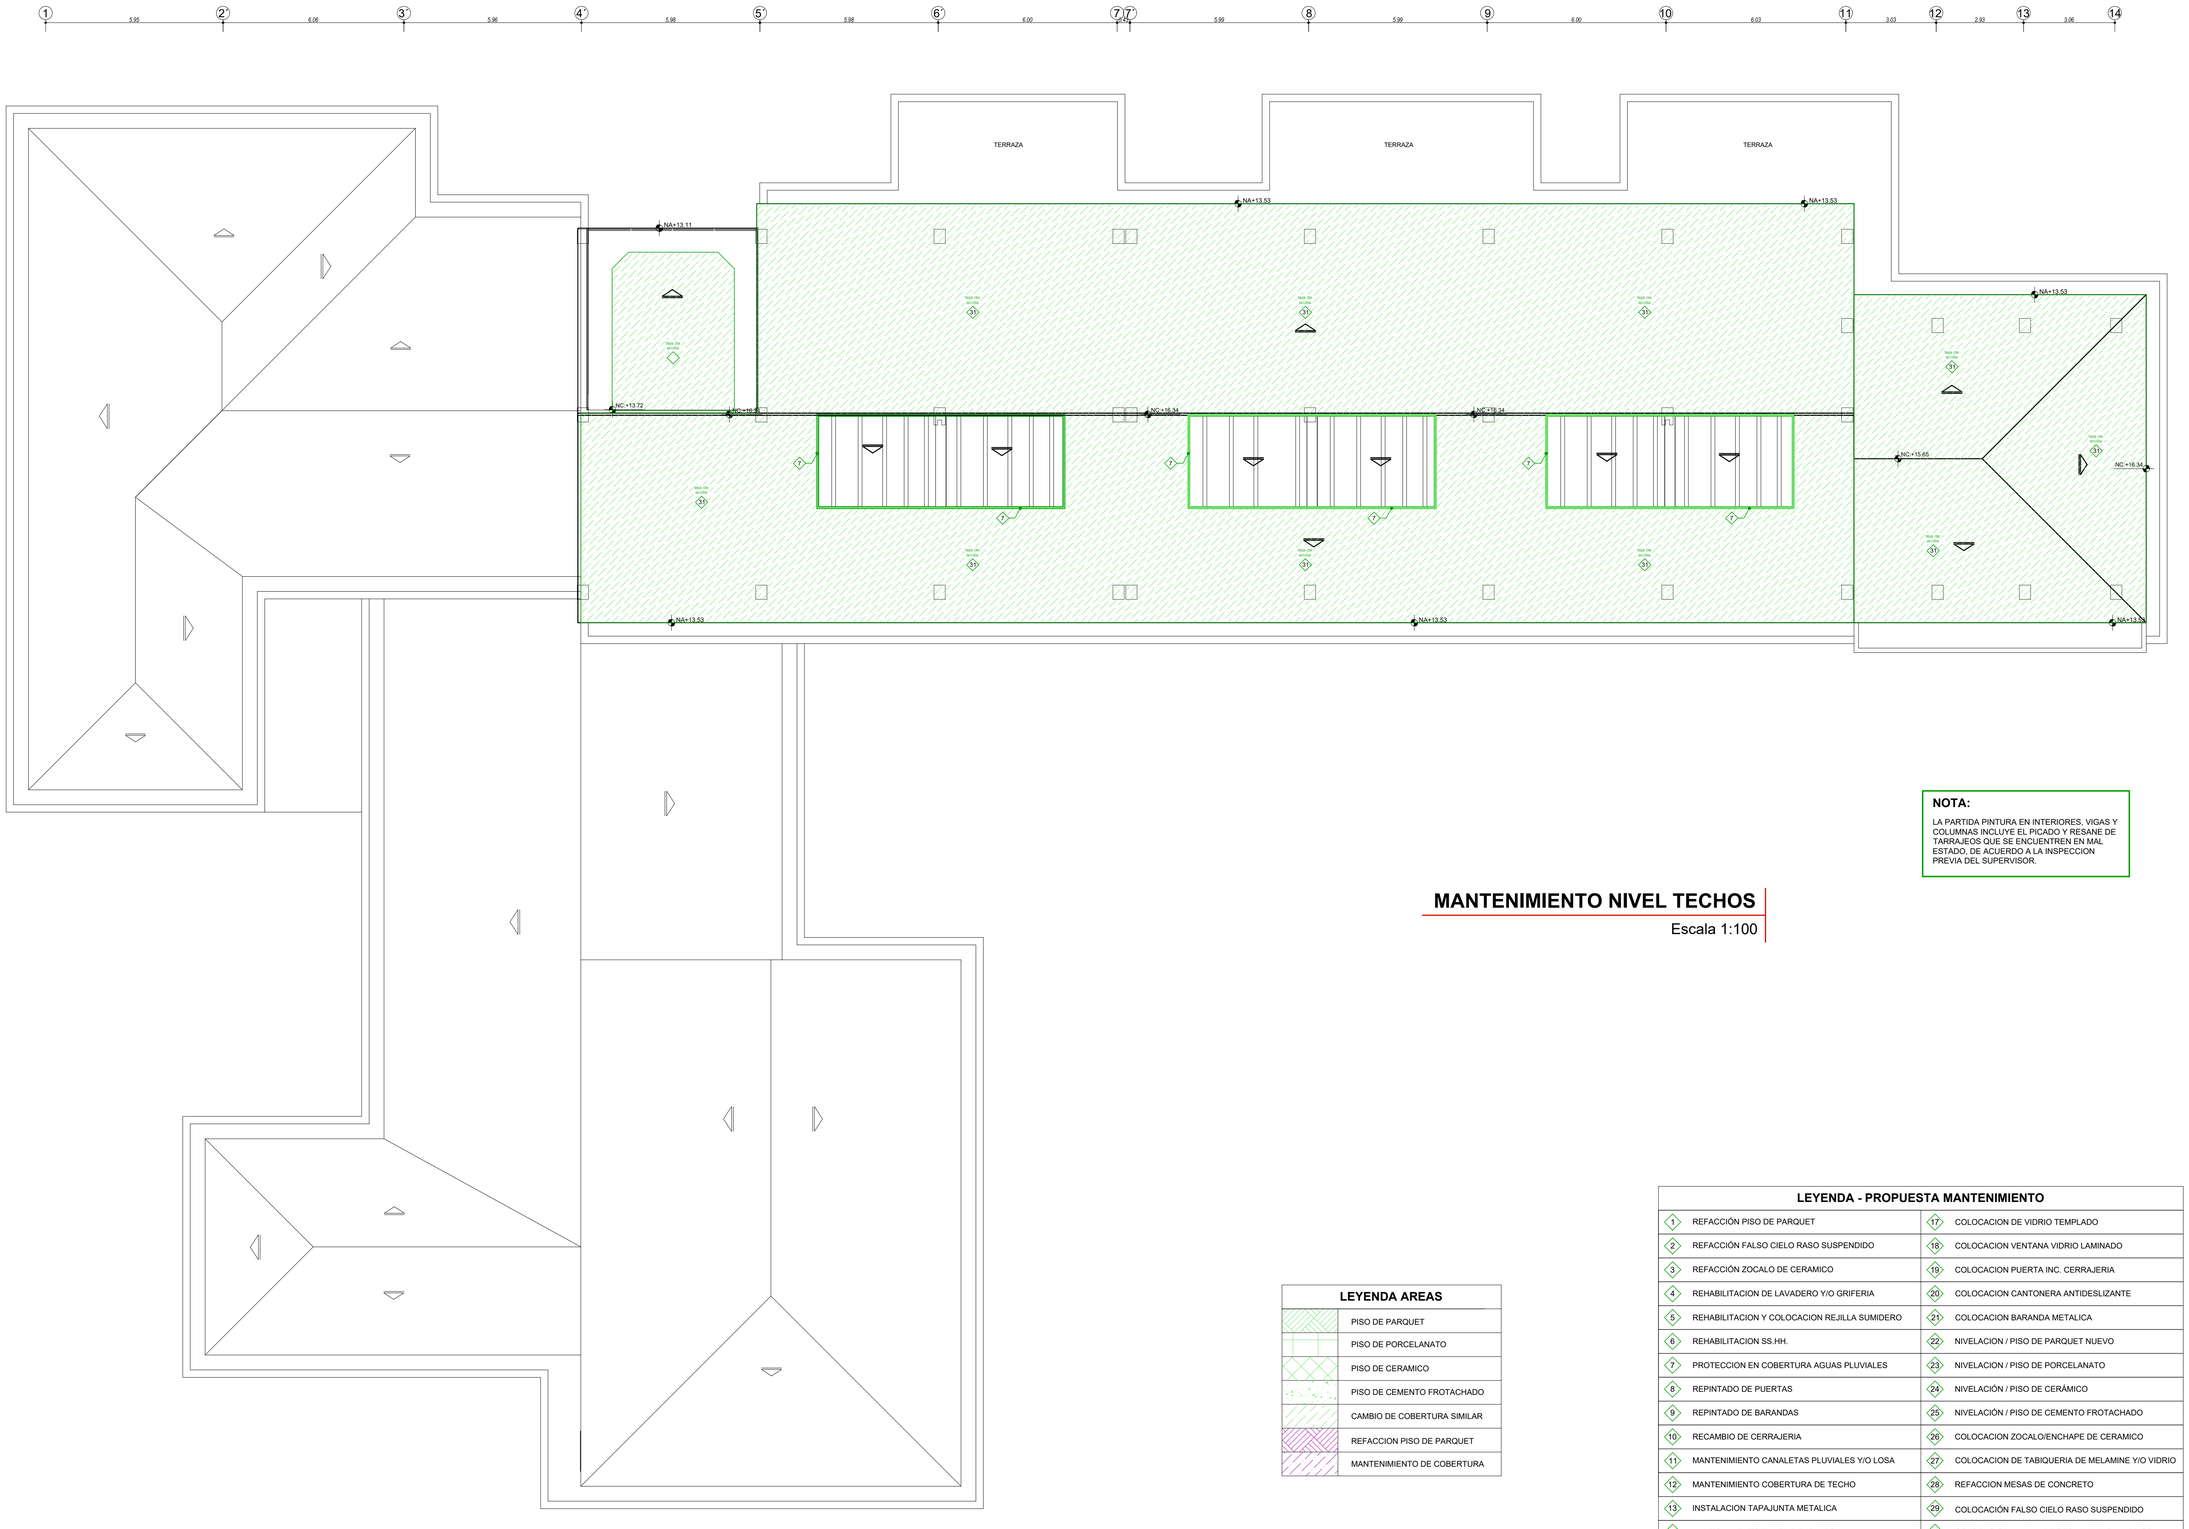

MANTENIMIENTO NIVEL TECHOS

Escala 1:100

NOTA:

LA PARTIDA PINTURA EN INTERIORES, VIGAS Y COLUMNAS INCLUYE EL PICADO Y RESANE DE TARRAJEOS QUE SE ENCUENTREN EN MAL ESTADO, DE ACUERDO A LA INSPECCION PREVIA DEL SUPERVISOR.

LEYENDA AREAS	
	PISO DE PARQUET
	PISO DE PORCELANATO
	PISO DE CERAMICO
	PISO DE CEMENTO FROTACHADO
	CAMBIO DE COBERTURA SIMILAR
	REFACCION PISO DE PARQUET
	MANTENIMIENTO DE COBERTURA

LEYENDA - PROPUESTA MANTENIMIENTO			
1	REFACCIÓN PISO DE PARQUET	17	COLOCACION DE VIDRIO TEMPLADO
2	REFACCIÓN FALSO CIELO RASO SUSPENDIDO	18	COLOCACION VENTANA VIDRIO LAMINADO
3	REFACCIÓN ZOCALO DE CERAMICO	19	COLOCACION PUERTA INC. CERRAJERIA
4	REHABILITACION DE LAVADERO Y/O GRIFERIA	20	COLOCACION CANTONERA ANTIDESLIZANTE
5	REHABILITACION Y COLOCACION REJILLA SUMIDERO	21	COLOCACION BARANDA METALICA
6	REHABILITACION SS.HH.	22	NIVELACION / PISO DE PARQUET NUEVO
7	PROTECCION EN COBERTURA AGUAS PLUVIALES	23	NIVELACION / PISO DE PORCELANATO
8	REPINTADO DE PUERTAS	24	NIVELACIÓN / PISO DE CERÁMICO
9	REPINTADO DE BARANDAS	25	NIVELACIÓN / PISO DE CEMENTO FROTACHADO
10	RECAMBIO DE CERRAJERIA	26	COLOCACION ZOCALO/ENCHAPE DE CERAMICO
11	MANTENIMIENTO CANALETAS PLUVIALES Y/O LOSA	27	COLOCACION DE TABIQUERIA DE MELAMINE Y/O VIDRIO
12	MANTENIMIENTO COBERTURA DE TECHO	28	REFACCION MESAS DE CONCRETO
13	INSTALACION TAPAJUNTA METALICA	29	COLOCACIÓN FALSO CIELO RASO SUSPENDIDO
14	MANTENIMIENTO TANQUE ELEVADO	30	COLOCACION LAMINA DE SEGURIDAD EN VIDRIOS
15	CERRAMIENTO DE MURO	31	INSTALACION DE COBERTURA NUEVA
16	COLOCACION APARATO SANITARIO	32	TARRAJEO CON IMPERMEABILIZANTE

ENTIDAD:

UNIVERSIDAD NACIONAL DE SAN ANTONIO ABAD DEL CUSCO

PROYECTO:

"SERVICIO DE CONSULTORIA PARA LA ELABORACION DEL EXPEDIENTE DE REHABILITACIÓN Y DIAGNOSTICO CON FINES DE LICENCIAMIENTO DE LA INFRAESTRUCTURA DE LA UNIVERSIDAD NACIONAL DE SAN ANTONIO ABAD DEL CUSCO" - ITEM 4

REGION: CUSCO

DEPARTAMENTO: CUSCO

PROVINCIA: CUSCO

DISTRITO: CUSCO

LOCALIDAD: PERAYOC

FACULTAD: ARQUITECTURA E INGENIERÍA CIVIL

ESCUELA PROFESIONAL: ARQUITECTURA

LUGAR: PABELLON ESCUELA PROFESIONAL DE ARQUITECTURA

CONSULTOR: CONSORCIO ROJAS SOTO

EXPEDIENTE: REHABILITACION

PLANO: MANTENIMIENTO TECHOS

DIBUJO:

ESCALA: INDICADA

FECHA: NOVIEMBRE 2017

AM.05