



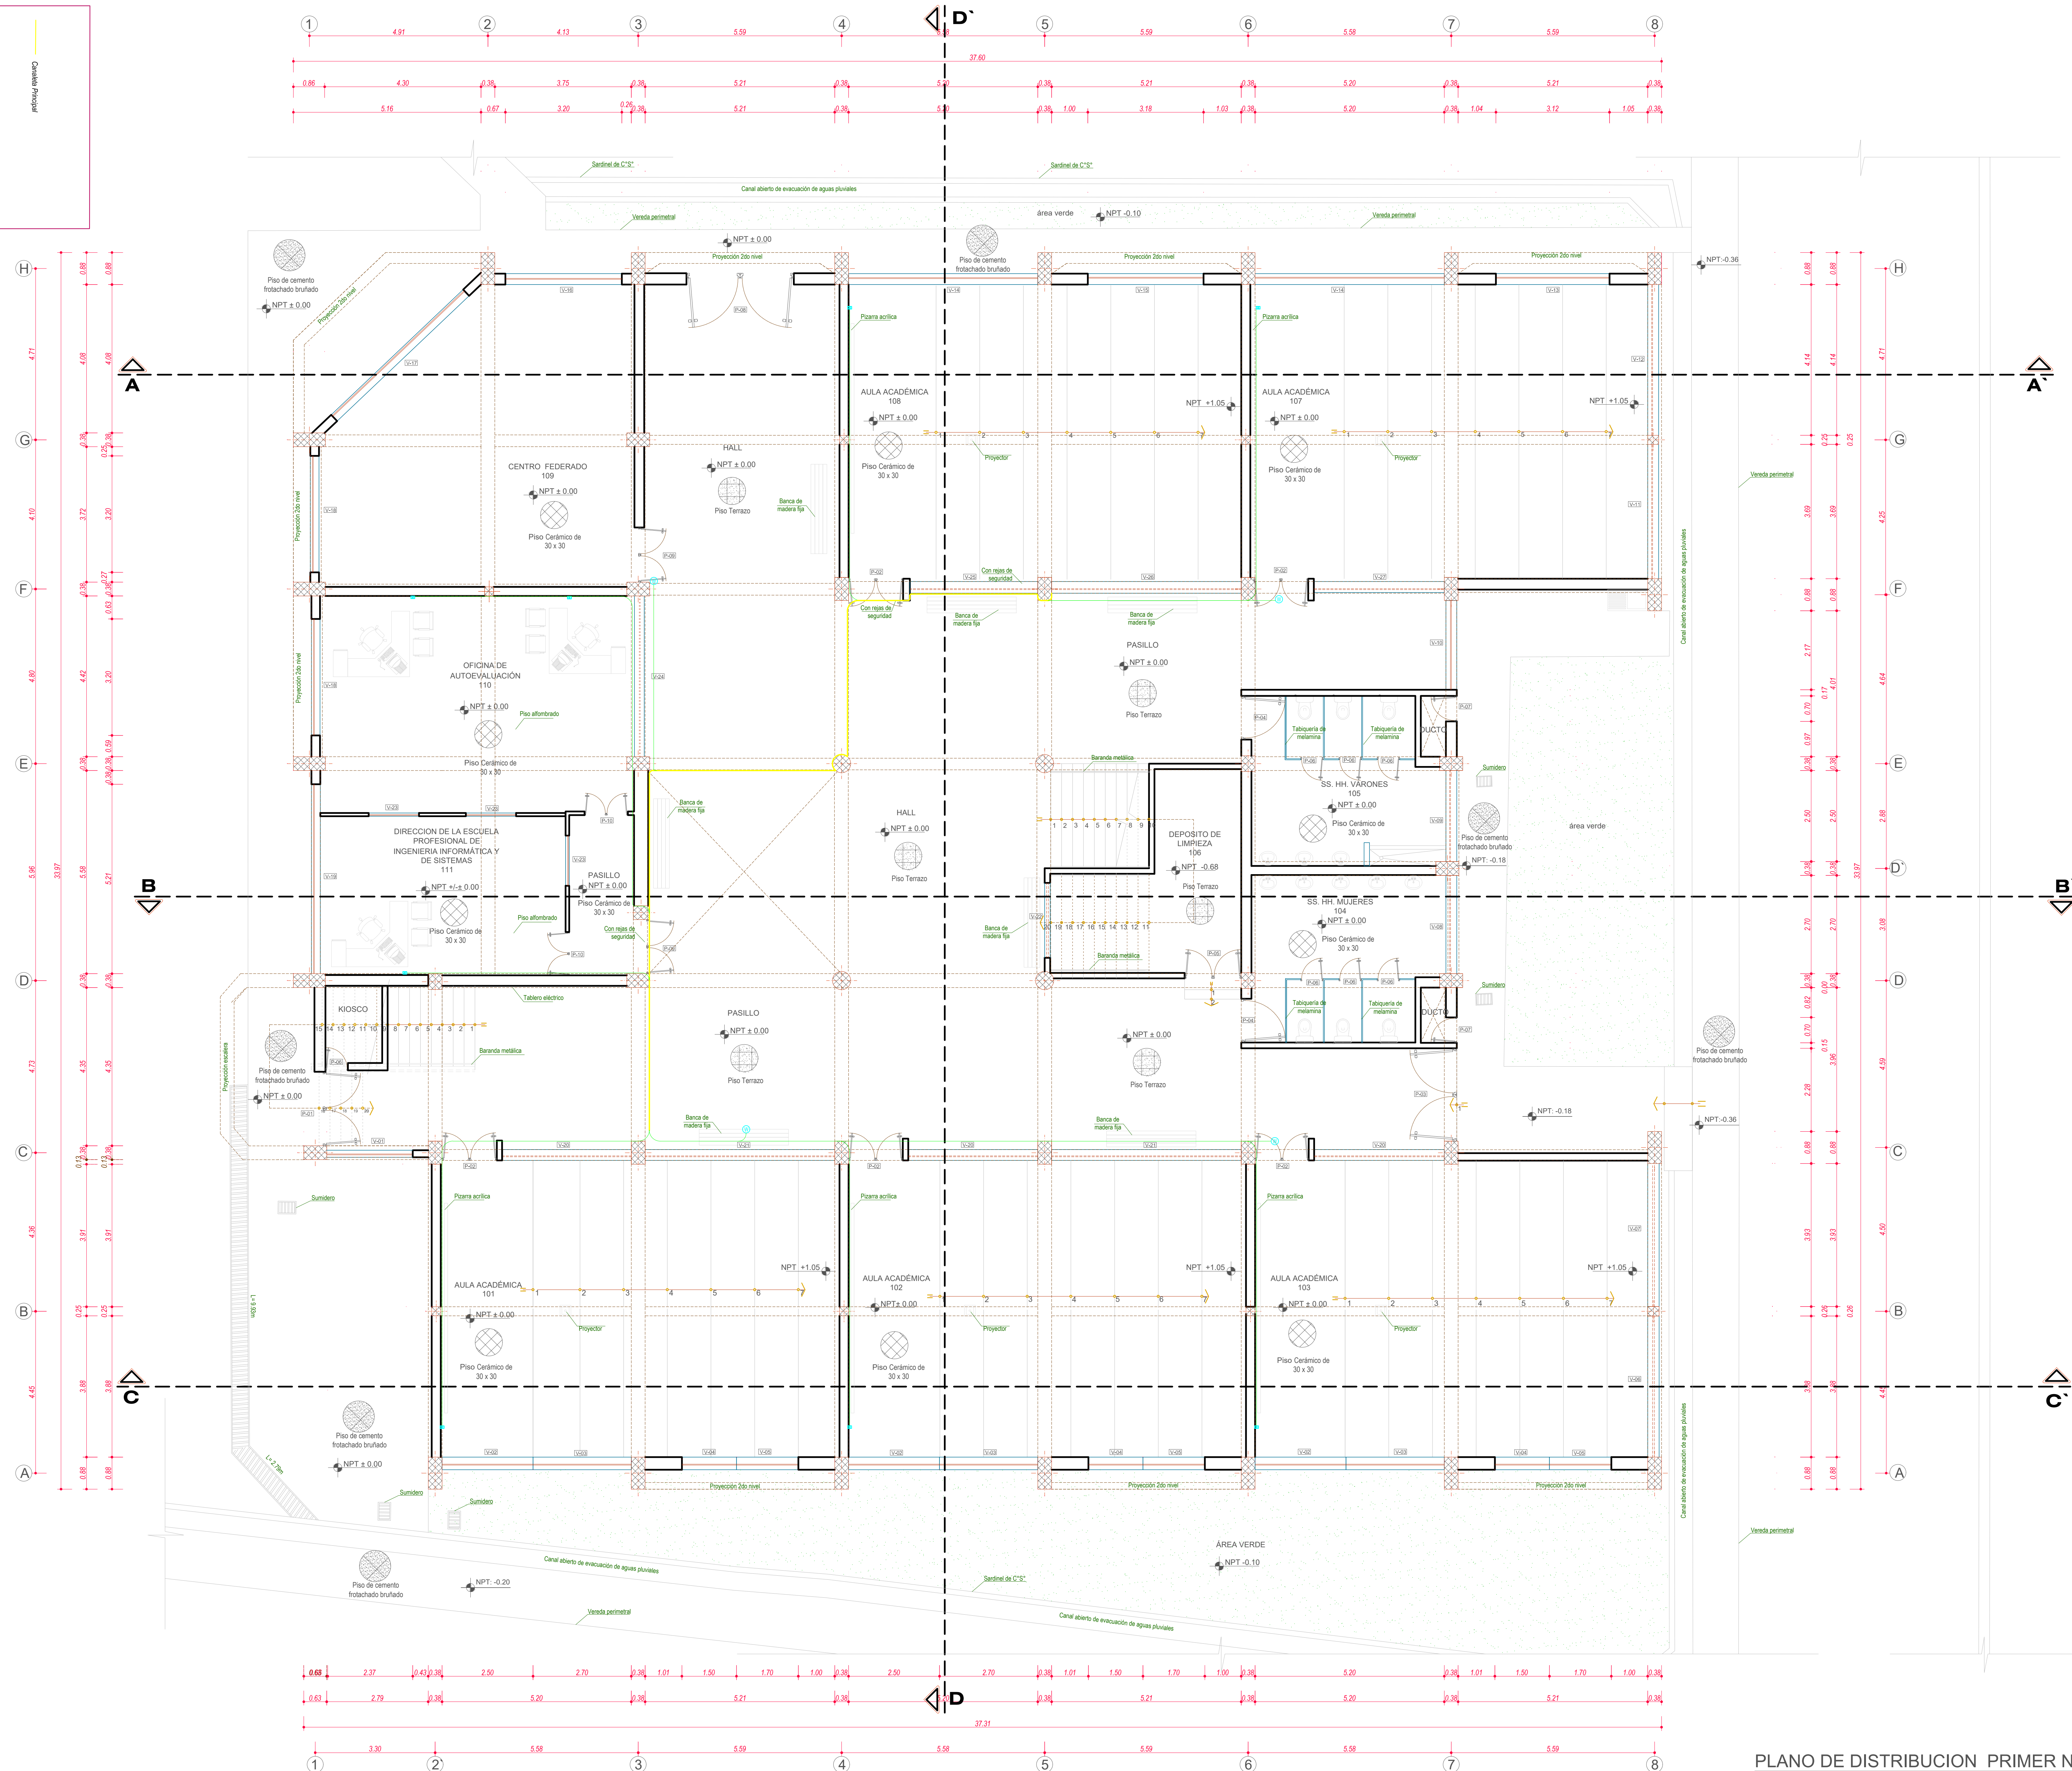

CODIGO	ANCHO	ALTO
P-1	2.08	2.60
P-2	1.51	2.80
P-3	2.55	2.60
P-4	1.00	2.80
P-5	1.55	2.10
P-6	0.62	2.50
P-7	0.70	1.75
P-8	2.95	2.80
P-9	1.50	2.60
P-10	1.19	3.20

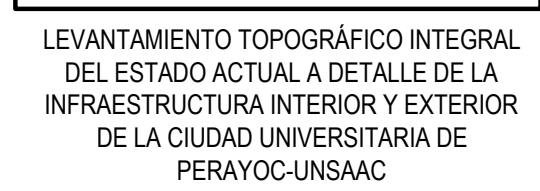

PLANO:

**PLANO DE DISTRIBUCION
PRIMER NIVEL**

JEFE DE PROYECTO:		
Arqto.	JORGE SALCEDO OLISPE	CAP 5812
EQUIPO TÉCNICO:		
Arqto.	AMÉD TEDILO MOSCOSO TOLEDO	CAP 13096
Arqto.	NELIDA COANQUI SINCHI ROCA	CAP 12517
Arqto.	SOLANGE DIAZ CACERES	CAP 12616
Arqto.	WILMA CUSI DELGADO	CAP 12615
Arqto.	ILIAN CARLOS PAUCAR VEGA	CAP 11959
Boch. Arqto.	JANIA CUSCUSPE OLISPE	
Boch. Arqto.	DANDY BARRENTOS RAMOS	
Boch. Arqto.	ADRIANA AJOLPA ALOSILLA	
Boch. Arqto.	KENY CHIQUE INCACUTIPA	
Asist.	JHONATAN CASAVEDE COOICA	

USUARIO:		LABIO:
UNIDAD UNIVERSITARIA DE PERAYCO		P-09
Distrito : CUSCO		
Provincia : CUSCO		
Departamento : CUSCO		
ESCALA:		
INDICADAS		
FECHA:		
Cusco, Diciembre del 2016		AR - 01