



CUADRO DE VANOS						
CODIGO	ALFEIZER	ANCHO	ALTO	CODIGO	ANCHO	ALTO
V-29	0.80	2.50	1.00	P-4	1.00	2.80
V-30	variable	2.50	1.00	P-5	0.62	2.50
V-31	variable	2.50	1.00	P-6	0.62	2.50
V-32	variable	1.70	1.80	P-14	1.89	2.25
V-36	1.26	2.70	0.99	P-15	0.89	2.80
V-37	1.26	2.50	0.99	P-16	0.85	2.25
V-38	1.26	2.50	0.99	P-17	0.80	2.80
V-41	1.85	3.60	0.75	P-18	1.49	2.60
V-42	1.50	4.14	0.75	M-1	1.49	2.60
V-43	0.80	3.12	1.00	M-3	4.16	2.08
V-45	0.80	3.20	1.00			
V-46	0.80	3.20	1.00			
V-47	0.80	2.62	1.00			
V-48	0.80	3.50	1.60			
V-50	0.80	5.24	1.60			
V-55	0.80	5.24	1.60			
V-56	0.45	0.30	1.80			
V-57	0.45	0.45	1.80			
V-58	0.44	5.03	1.96			
V-59	0.44	5.46	1.81			
V-60	1.00	0.90	1.40			
V-62	1.00	2.37	1.60			
V-63	1.05	3.88	0.75			
V-64	1.05	3.93	0.75			
V-65	variable	3.48	0.75			
V-66	1.00	3.50	0.86			
V-67	1.00	3.55	0.90			
V-68	1.00	3.59	0.90			
V-69	1.00	3.58	0.90			
V-71	1.65	3.70	0.74			
V-72	0.95	1.75	1.30			
V-73	1.00	0.90	1.30			

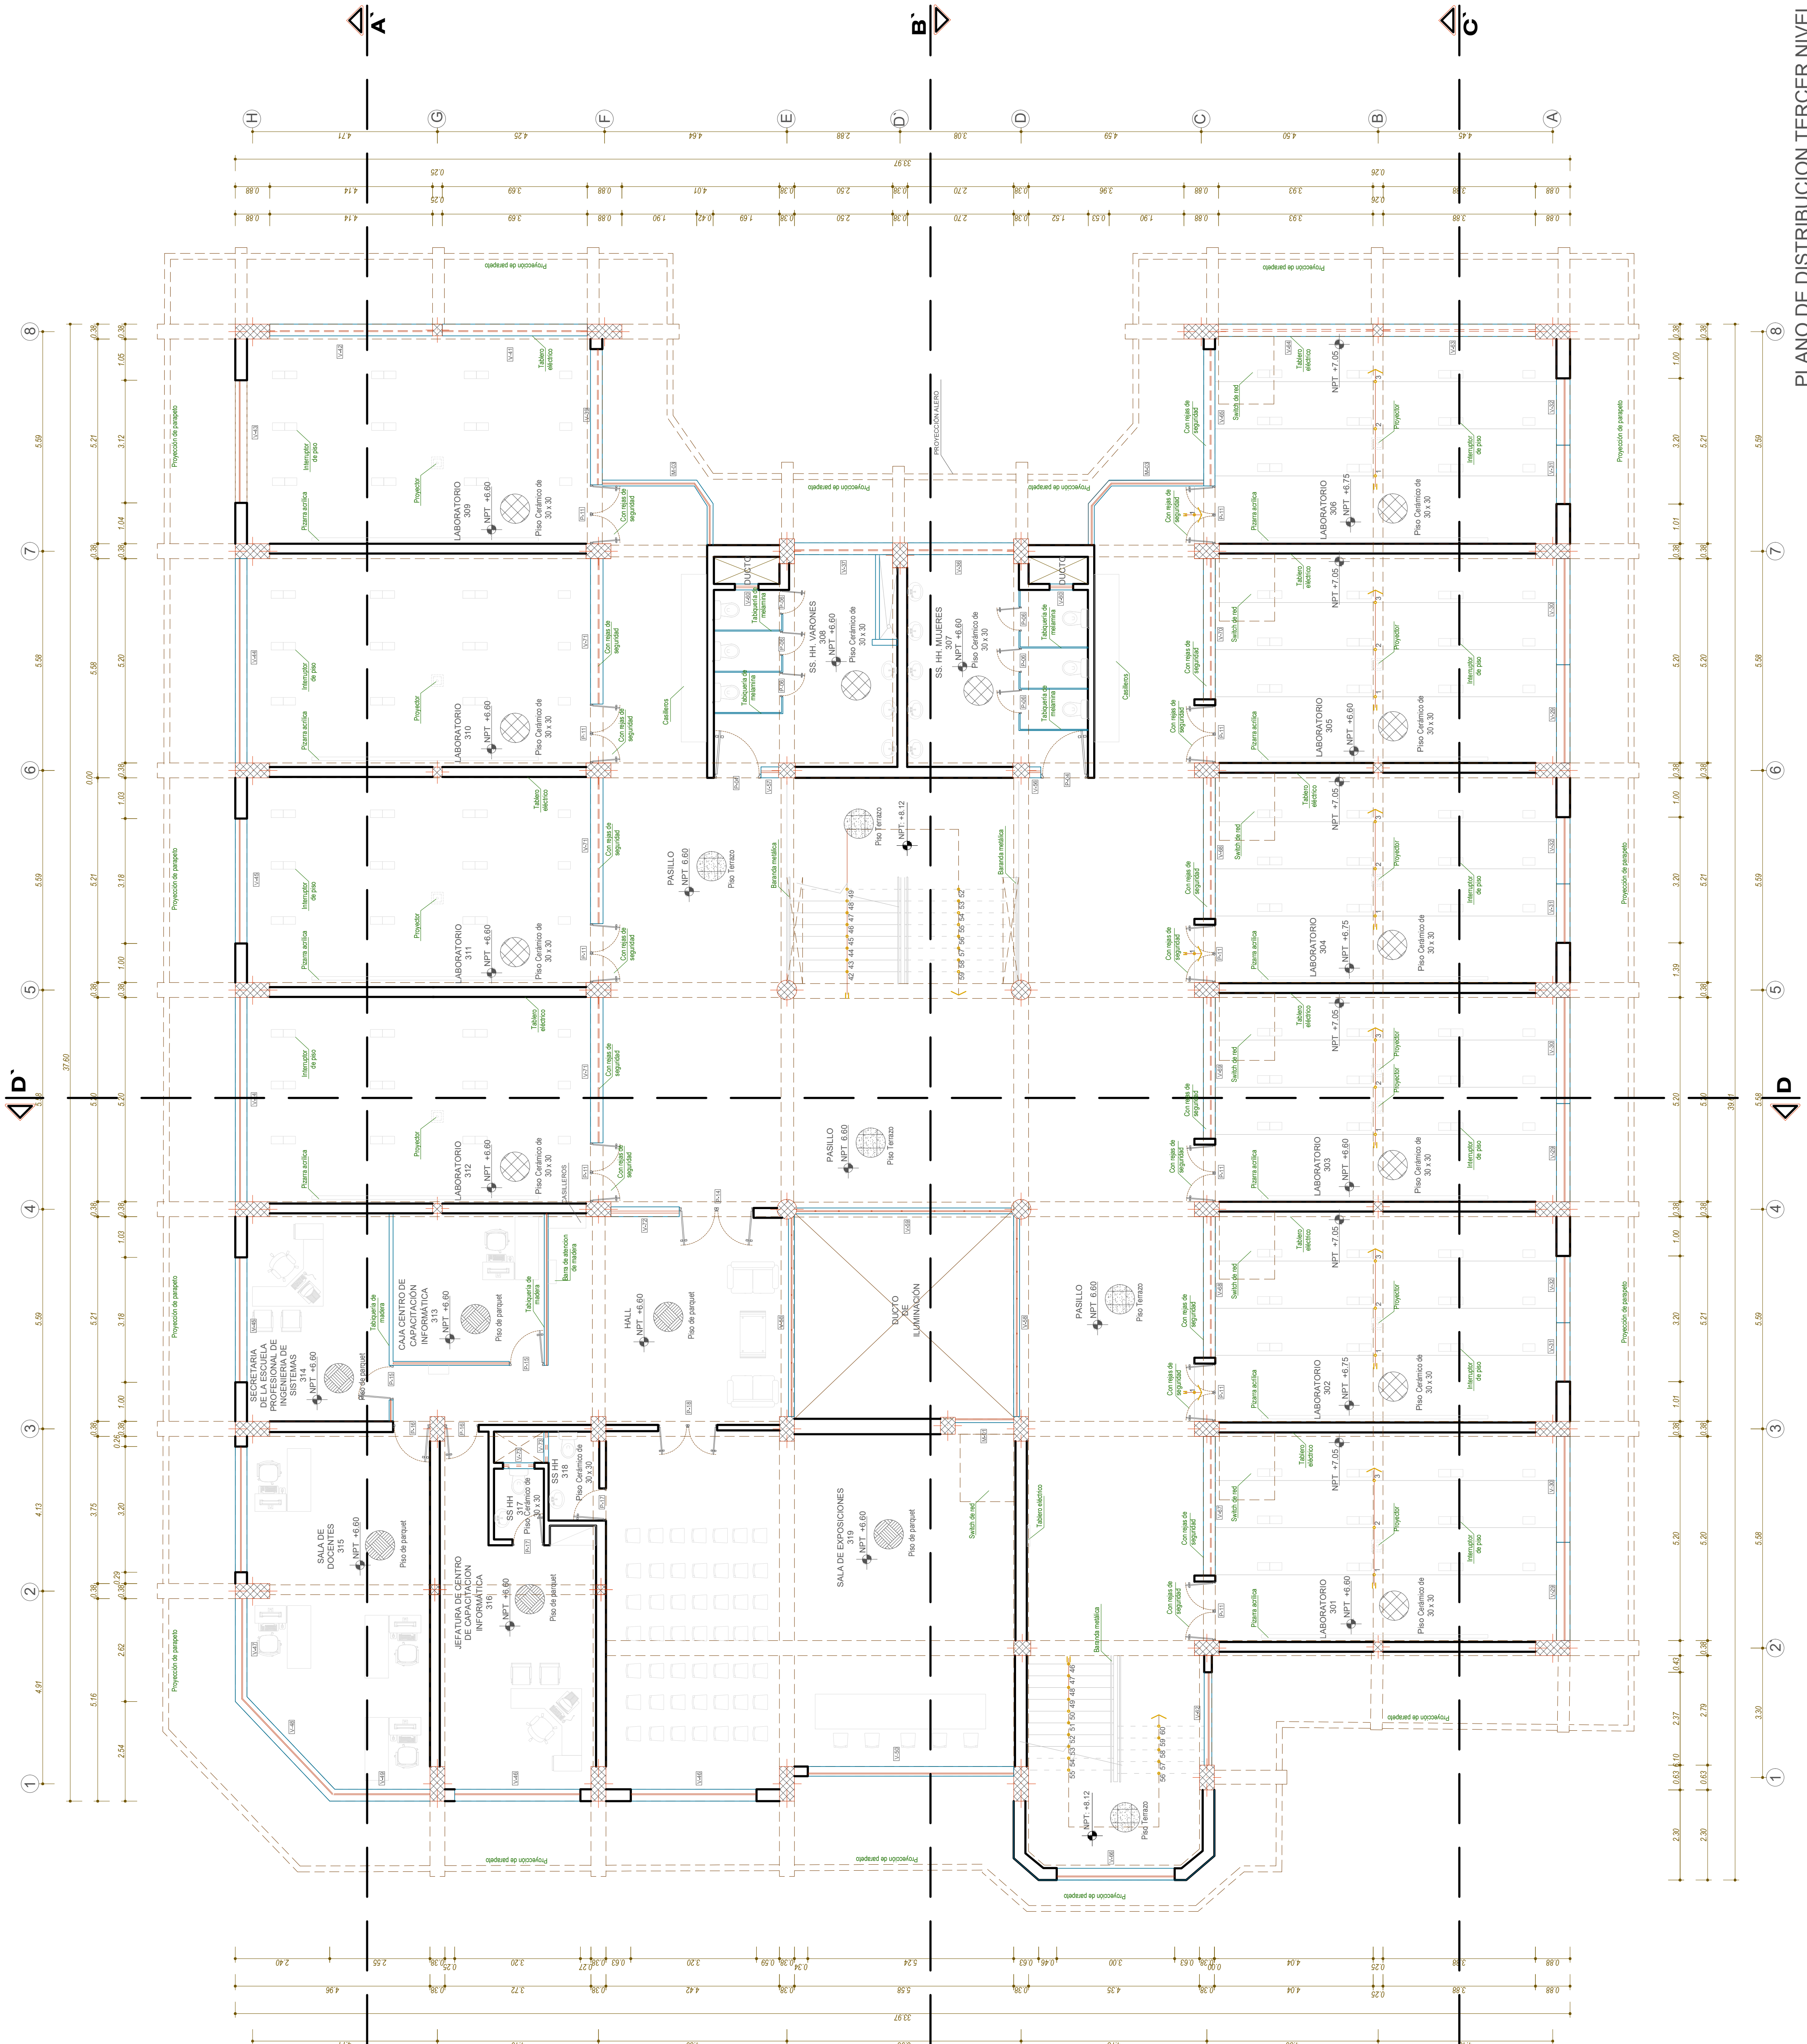

PLANO DE DISTRIBUCION TERCER NIVEL

ESQ. 1/15

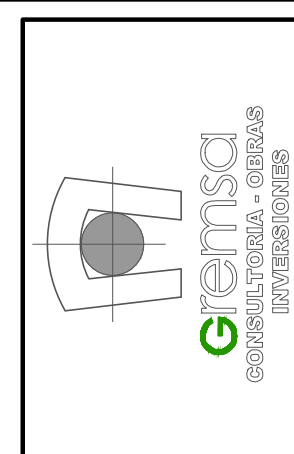

LEVANTAMIENTO DEL PLAN DE DISTRIBUCION TERCER NIVEL DE LA CIUDAD UNIVERSITARIA DE PUNTA CANAS

08. INFORMATICA Y SISTEMAS

PLANO

PROYECTO	PROYECTO	PROYECTO	PROYECTO	PROYECTO
PROYECTO	PROYECTO	PROYECTO	PROYECTO	PROYECTO
AR - 03