


CUADRO DE VANOS					
CODIGO	ALFEIZER	ANCHO	ALTO	CODIGO	ANCHO
V-29	0.80	2.50	1.60	P-4	1.00
V-30	variable	2.70	1.60	P-6	0.62
V-31	variable	1.50	1.60	P-11	1.51
V-32	variable	1.70	1.60	P-14	1.89
V-36	1.25	2.70	0.99	P-15	0.90
V-37	1.25	2.50	0.99	P-16	0.95
V-39	1.68	3.50	0.72	P-17	0.80
V-41	1.85	3.89	0.75	P-18	1.50
V-42	1.50	4.14	0.75	M-1	1.49
V-43	0.80	3.12	1.60	M-3	4.16
V-44	0.80	5.20	1.60		
V-45	0.80	3.18	1.60		
V-46	0.80	3.30	1.60		
V-47	0.80	2.62	1.60		
V-48	0.80	3.50	1.60		
V-49	0.80	2.55	1.60		
V-50	0.80	5.24	1.60		
V-56	0.45	0.30	1.60		
V-57	0.45	0.45	1.80		
V-58	0.44	5.03	1.96		
V-59	0.44	5.46	1.81		
V-60	1.00	0.60	1.40		
V-62	0.40	2.37	1.60		
V-63	1.05	3.88	0.75		
V-64	1.05	3.93	0.75		
V-65	variable	3.45	0.75		
V-66	1.00	3.00	1.86		
V-67	1.90	3.55	0.50		
V-68	1.90	3.59	0.50		
V-69	1.90	3.60	0.50		
V-70	1.90	3.58	0.50		
V-71	1.66	3.70	0.74		
V-72	0.95	3.75	1.30		
V-73	1.00	0.60	1.30		

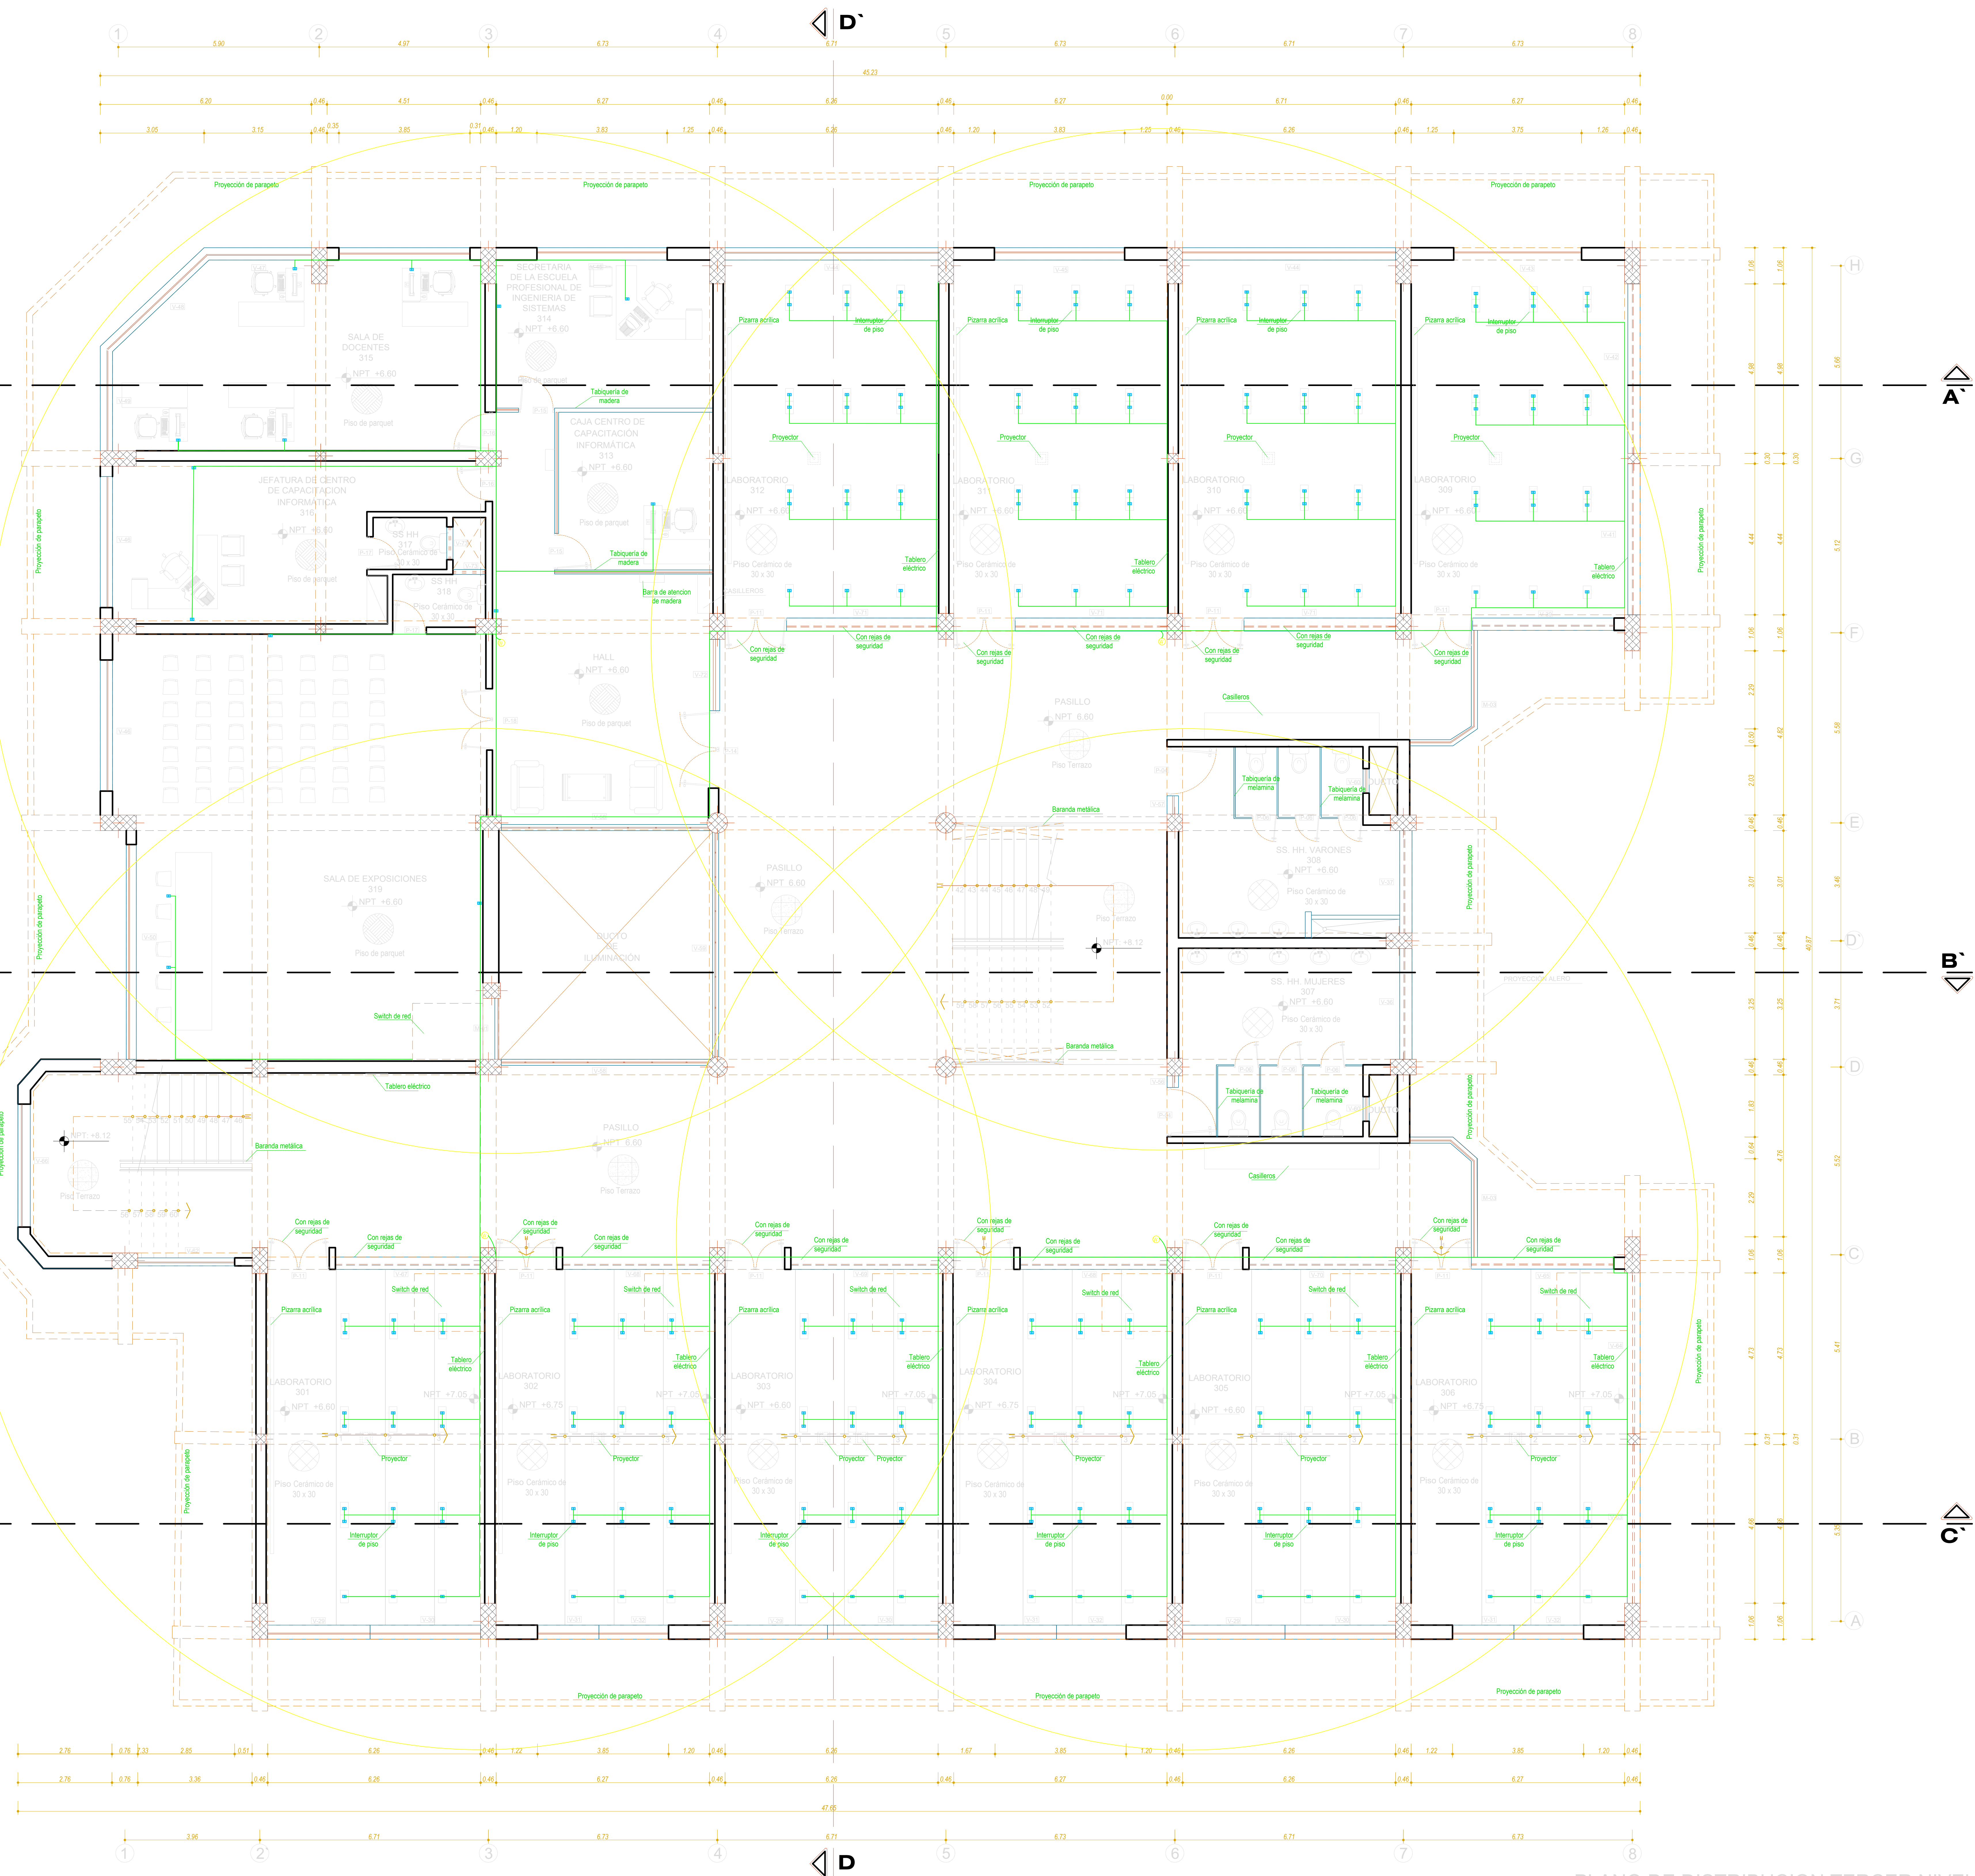

LEYENDA

- Toma de Datos Doble Cat 6A (Dos puertos RJ45)
- Punto para Access Point (Wi-Fi) (Un puerto RJ45)
- Punto para Cámara de Seguridad (CCTV) (Un puerto RJ45)



LEVANTAMIENTO TOPOGRÁFICO INTEGRAL DEL ESTADO ACTUAL A DETALLE DE LA INFRAESTRUCTURA INTERIOR Y EXTERIOR DE LA CIUDAD UNIVERSITARIA DE PERAYOC-UNSAAC

PABELLON:
09. INFORMATICA Y SISTEMAS

PLANO:
PLANO DE DISTRIBUCION TERCER NIVEL

ÁREAS PROYECTOS:	CAP
Área: JORGE SALCEDO GUSPTE	5812
Área: AMED TIEDILLO MOSCOSO TOLEDO	13006
Área: NELDA GONZALEZ ENRIQUE ROCA	12017
Área: SOLANGE DAZ CACERES	12814
Área: YUMA GUSI DELGADO	12815
Área: JUAN CARLOS PALACAR VEGA	11959
Área: JANA CLODIBERT GUSPTE	
Área: DANCY BARRENTOS RAMOS	
Área: ADRIANA ANDRADA ALONSO	
Área: KENY CHOQUE INCAJUTPA	
Área: ANTONIAN CASAREDE CODICIA	

UBICACIÓN:	LABORATORIO DE TRABAJO:	LABOR.
Dirección:	CUSCO	P-09
Dirección:	CUSCO	AR-03
Dirección:	CUSCO	
ESCALA:	INDICADAS	
FECHA:	Cusco, Diciembre del 2016	