


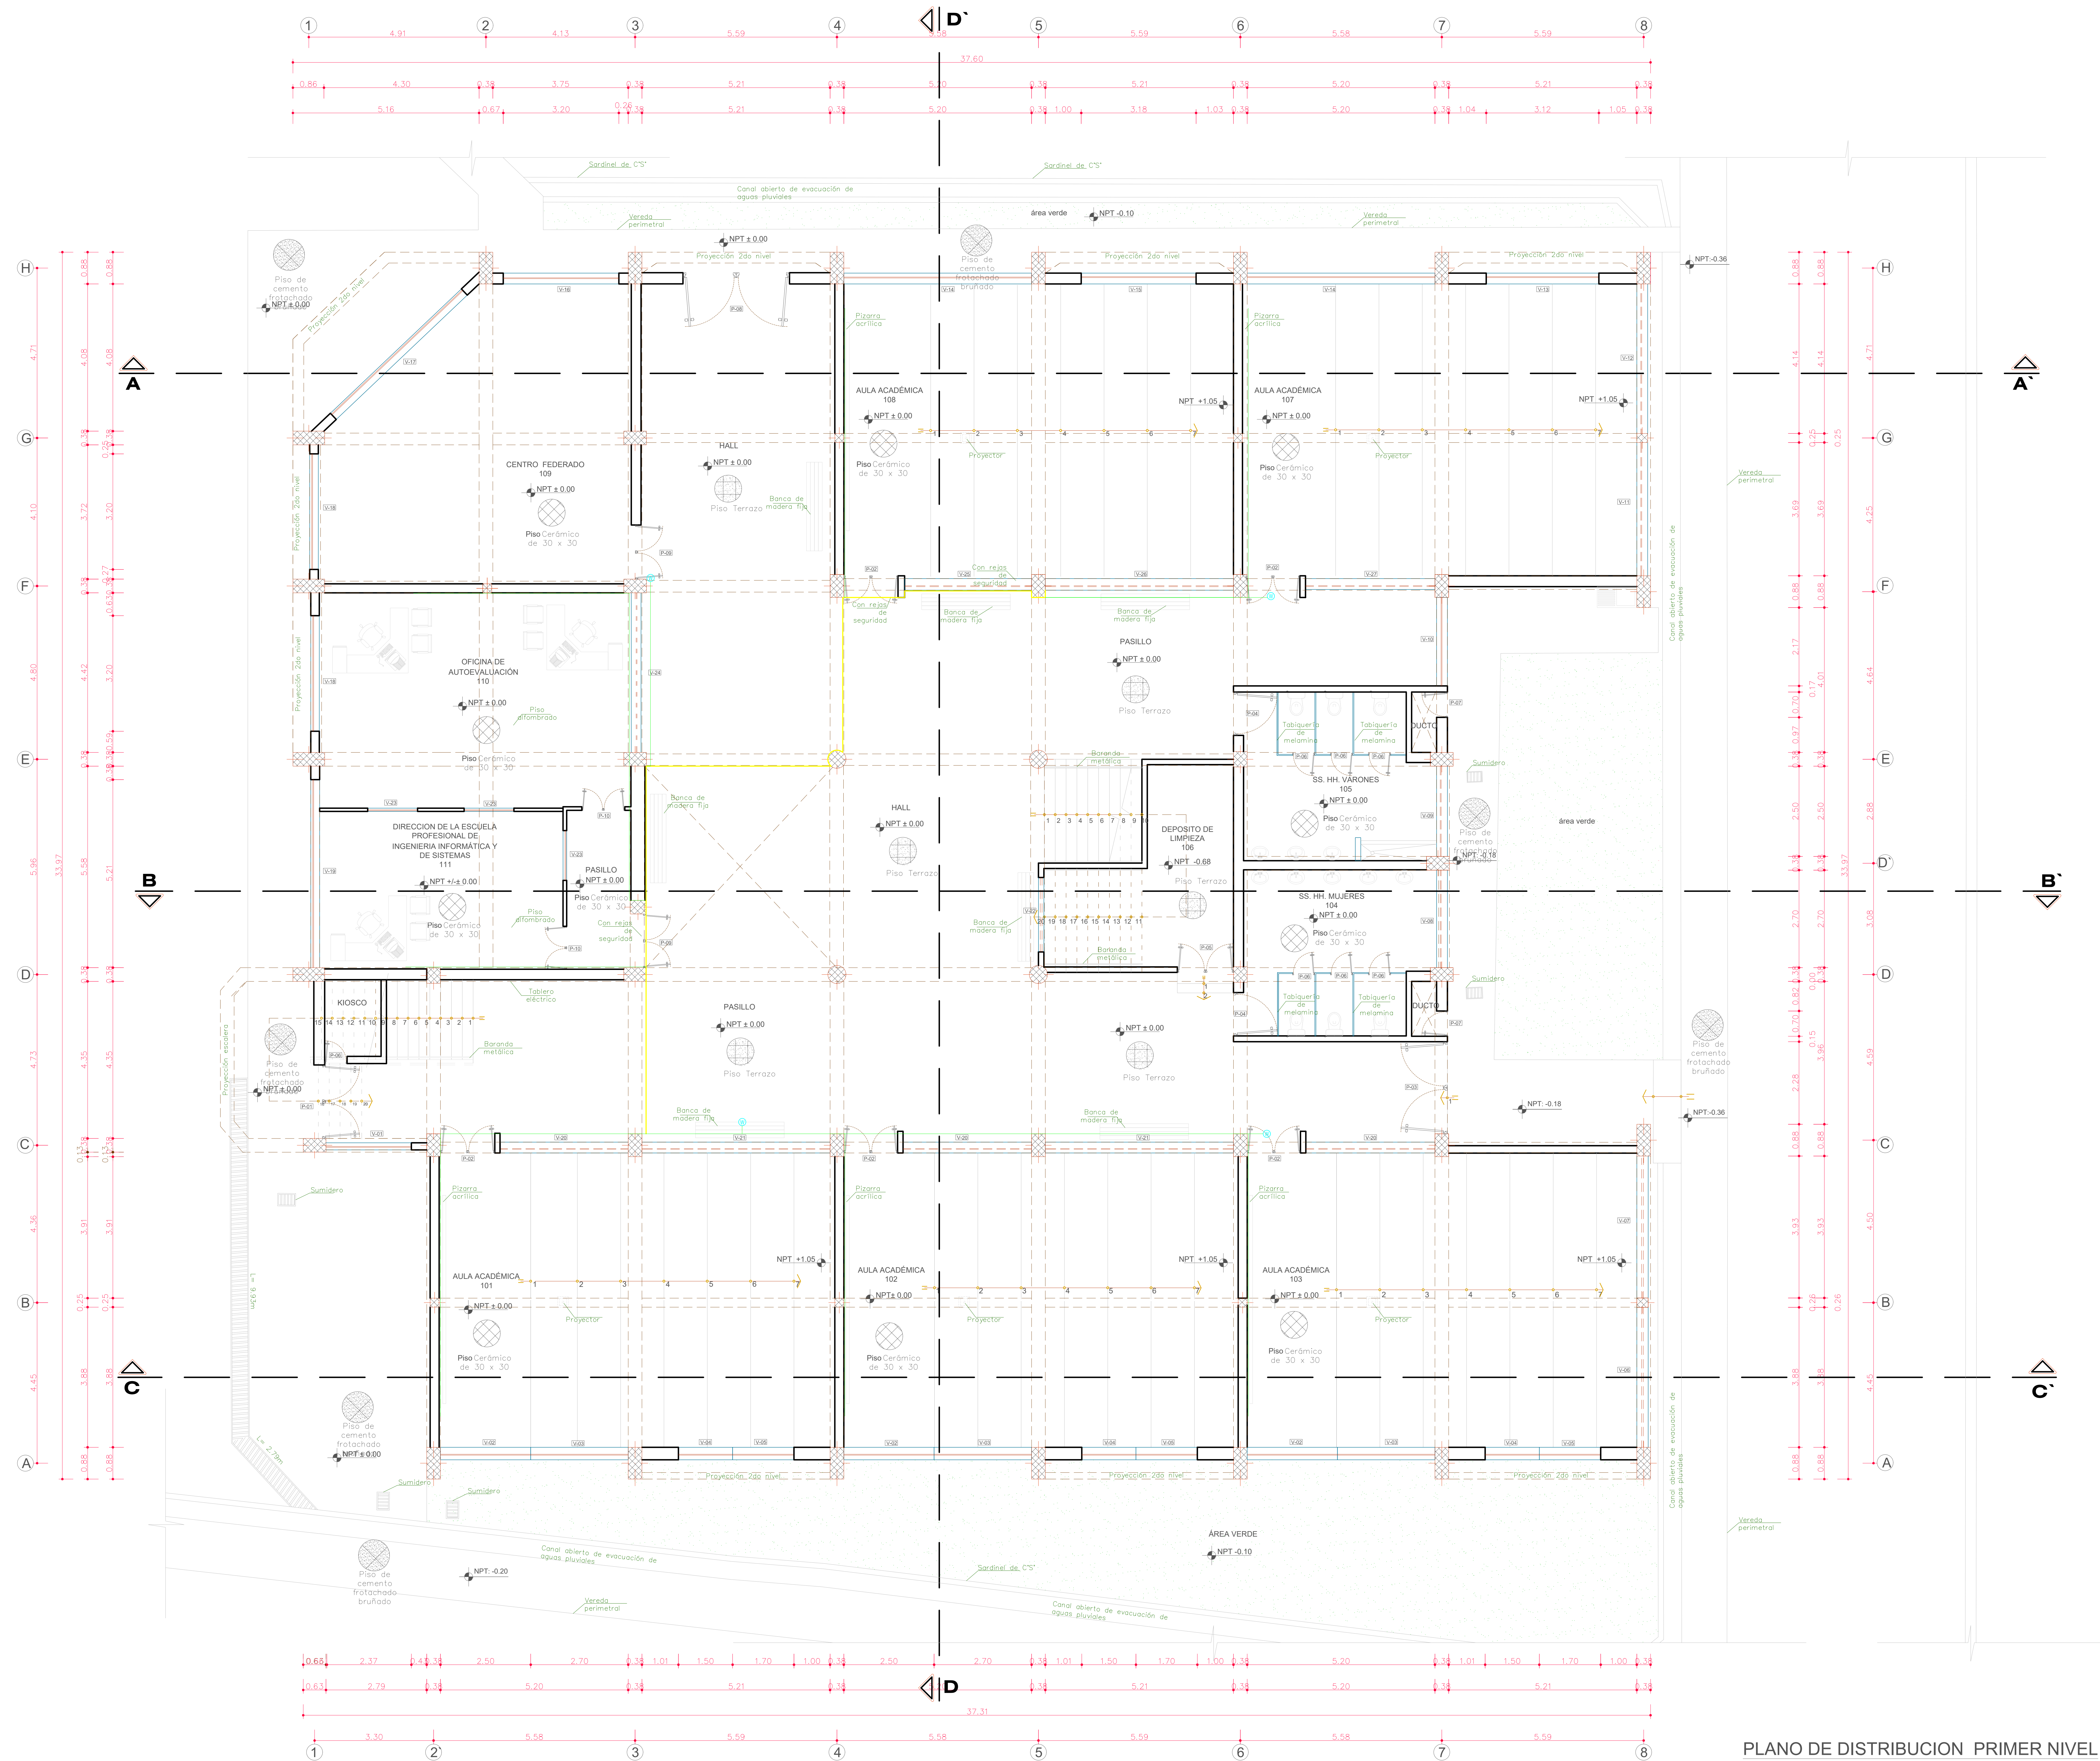

CUADRO DE VANOS			
CODIGO	ALFEIZER	ANCHO	ALTO
V-1	1.20	2.37	1.60
V-2	1.20	2.50	1.60
V-3	variable	2.70	1.60
V-4	variable	1.50	1.60
V-5	variable	1.70	1.60
V-6	1.80	3.88	0.75
V-7	1.80	3.93	0.75
V-8	1.30	2.70	1.30
V-9	1.22	2.50	1.38
V-10	0.90	2.17	1.70
V-11	1.80	3.69	0.75
V-12	1.85	4.14	0.75
V-13	variable	3.12	1.75
V-14	variable	5.20	1.75
V-15	variable	3.18	1.75
V-16	1.05	3.20	1.75
V-17	1.05	5.00	2.15
V-18	1.05	3.20	1.55
V-19	1.05	5.21	1.55
V-20	2.28	3.55	0.52
V-21	1.98	5.21	1.22
V-22	2.13	2.06	0.47
V-23	1.10	1.38	1.17
V-24	2.28	4.42	0.52
V-25	2.28	3.52	0.52
V-26	2.28	5.21	0.52
V-27	2.28	3.59	0.52

CUADRO DE VANOS		
CODIGO	ANCHO	ALTO
P-1	2.08	2.60
P-2	1.51	2.80
P-3	2.55	2.60
P-4	1.00	2.80
P-5	1.55	2.10
P-6	0.62	2.50
P-7	0.70	1.75
P-8	2.95	2.80
P-9	1.50	2.60
P-10	1.19	3.20

PLANO DE DISTRIBUCION PRIMER NIVEL
ESC:1/75

LEVANTAMIENTO TOPOGRÁFICO INTEGRAL DEL ESTADO ACTUAL A DETALLE DE LA INFRAESTRUCTURA INTERIOR Y EXTERIOR DE LA CIUDAD UNIVERSITARIA DE PERAYOC-UNSAAC DE INFORMATICA Y SISTEMAS

PLANO: PLANO DE DISTRIBUCION PRIMER NIVEL

ART. DE PROYECTO: JORGE SALCEDO QUISPE
 EQUIPO: CAP 5812
 ARQUITECTO: AMED TELLO MOSCOSO TOLEDO
 ARQUITECTO: NELSON BANGUO SANCHEZ ROSA
 ARQUITECTO: ALVARO DIAZ CACERES
 ARQUITECTO: JUAN CARLOS DELGADO
 ARQUITECTO: JUAN CARLOS PAUCAR VEGA
 BOCH: ANDY DANDY BARRENTOS RAMOS
 BOCH: ANDY ASRIANA AQUILA ALDILA
 BOCH: ANDY KENY CHOQUE INCAUTIPA
 ASIST. JONATAN CADAVEDE CODICA

UBICACION: CIUDAD UNIVERSITARIA DE PERAYOC-UNSAAC
 Distrito: CUSCO
 Provincia: CUSCO
 Departamento: CUSCO
 ESCALA: INDICADAS
 FECHA: Cusco, Diciembre del 2017