
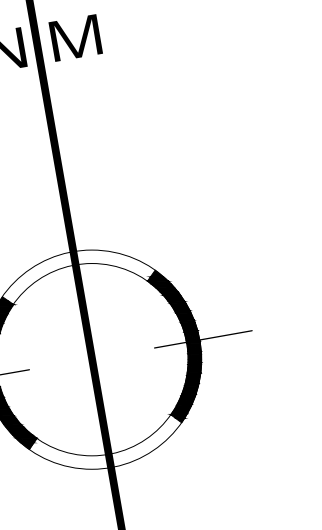


CUADRO DE VANOS					
CODIGO	ALFEIZER	ANCHO	ALTO	CODIGO	ANCHO
V-28	0.40	2.37	1.60	P-4	1.00
V-29	0.80	2.50	1.60	P-6	0.62
V-30	variable	2.70	1.60	P-11	1.51
V-31	variable	1.50	1.60	P-12	1.89
V-32	variable	1.70	1.60	P-13	0.82
V-33	0.45	3.88	0.75	M-1	1.49
V-34	0.45	3.93	0.75		
V-35	0.71	2.55	1.54		
V-36	1.26	2.70	0.99		
V-37	1.26	2.50	0.99		
V-38	0.71	2.45	1.54		
V-39	1.68	3.50	0.72		
V-40	variable	3.50	0.75		
V-41	1.85	3.69	0.75		
V-42	1.50	4.14	0.75		
V-43	0.80	3.12	1.60		
V-44	0.80	5.20	1.60		
V-45	0.80	3.18	1.60		
V-46	0.80	3.20	1.60		
V-47	0.80	2.62	1.60		
V-48	0.80	3.50	1.60		
V-49	0.80	2.55	1.60		
V-50	0.65	5.24	1.60		
V-51	1.00	3.00	1.18		
V-52	1.68	3.55	0.72		
V-53	1.68	5.21	0.72		
V-54	1.68	3.60	0.72		
V-55	1.68	3.58	0.72		
V-56	0.45	0.30	1.80		
V-57	0.45	0.45	1.80		
V-58	0.44	5.03	1.96		
V-59	0.44	5.46	1.81		
V-60	1.00	0.60	1.40		
V-61	1.68	3.71	0.72		
V-74	0.44	1.30	1.81		

A

B

C

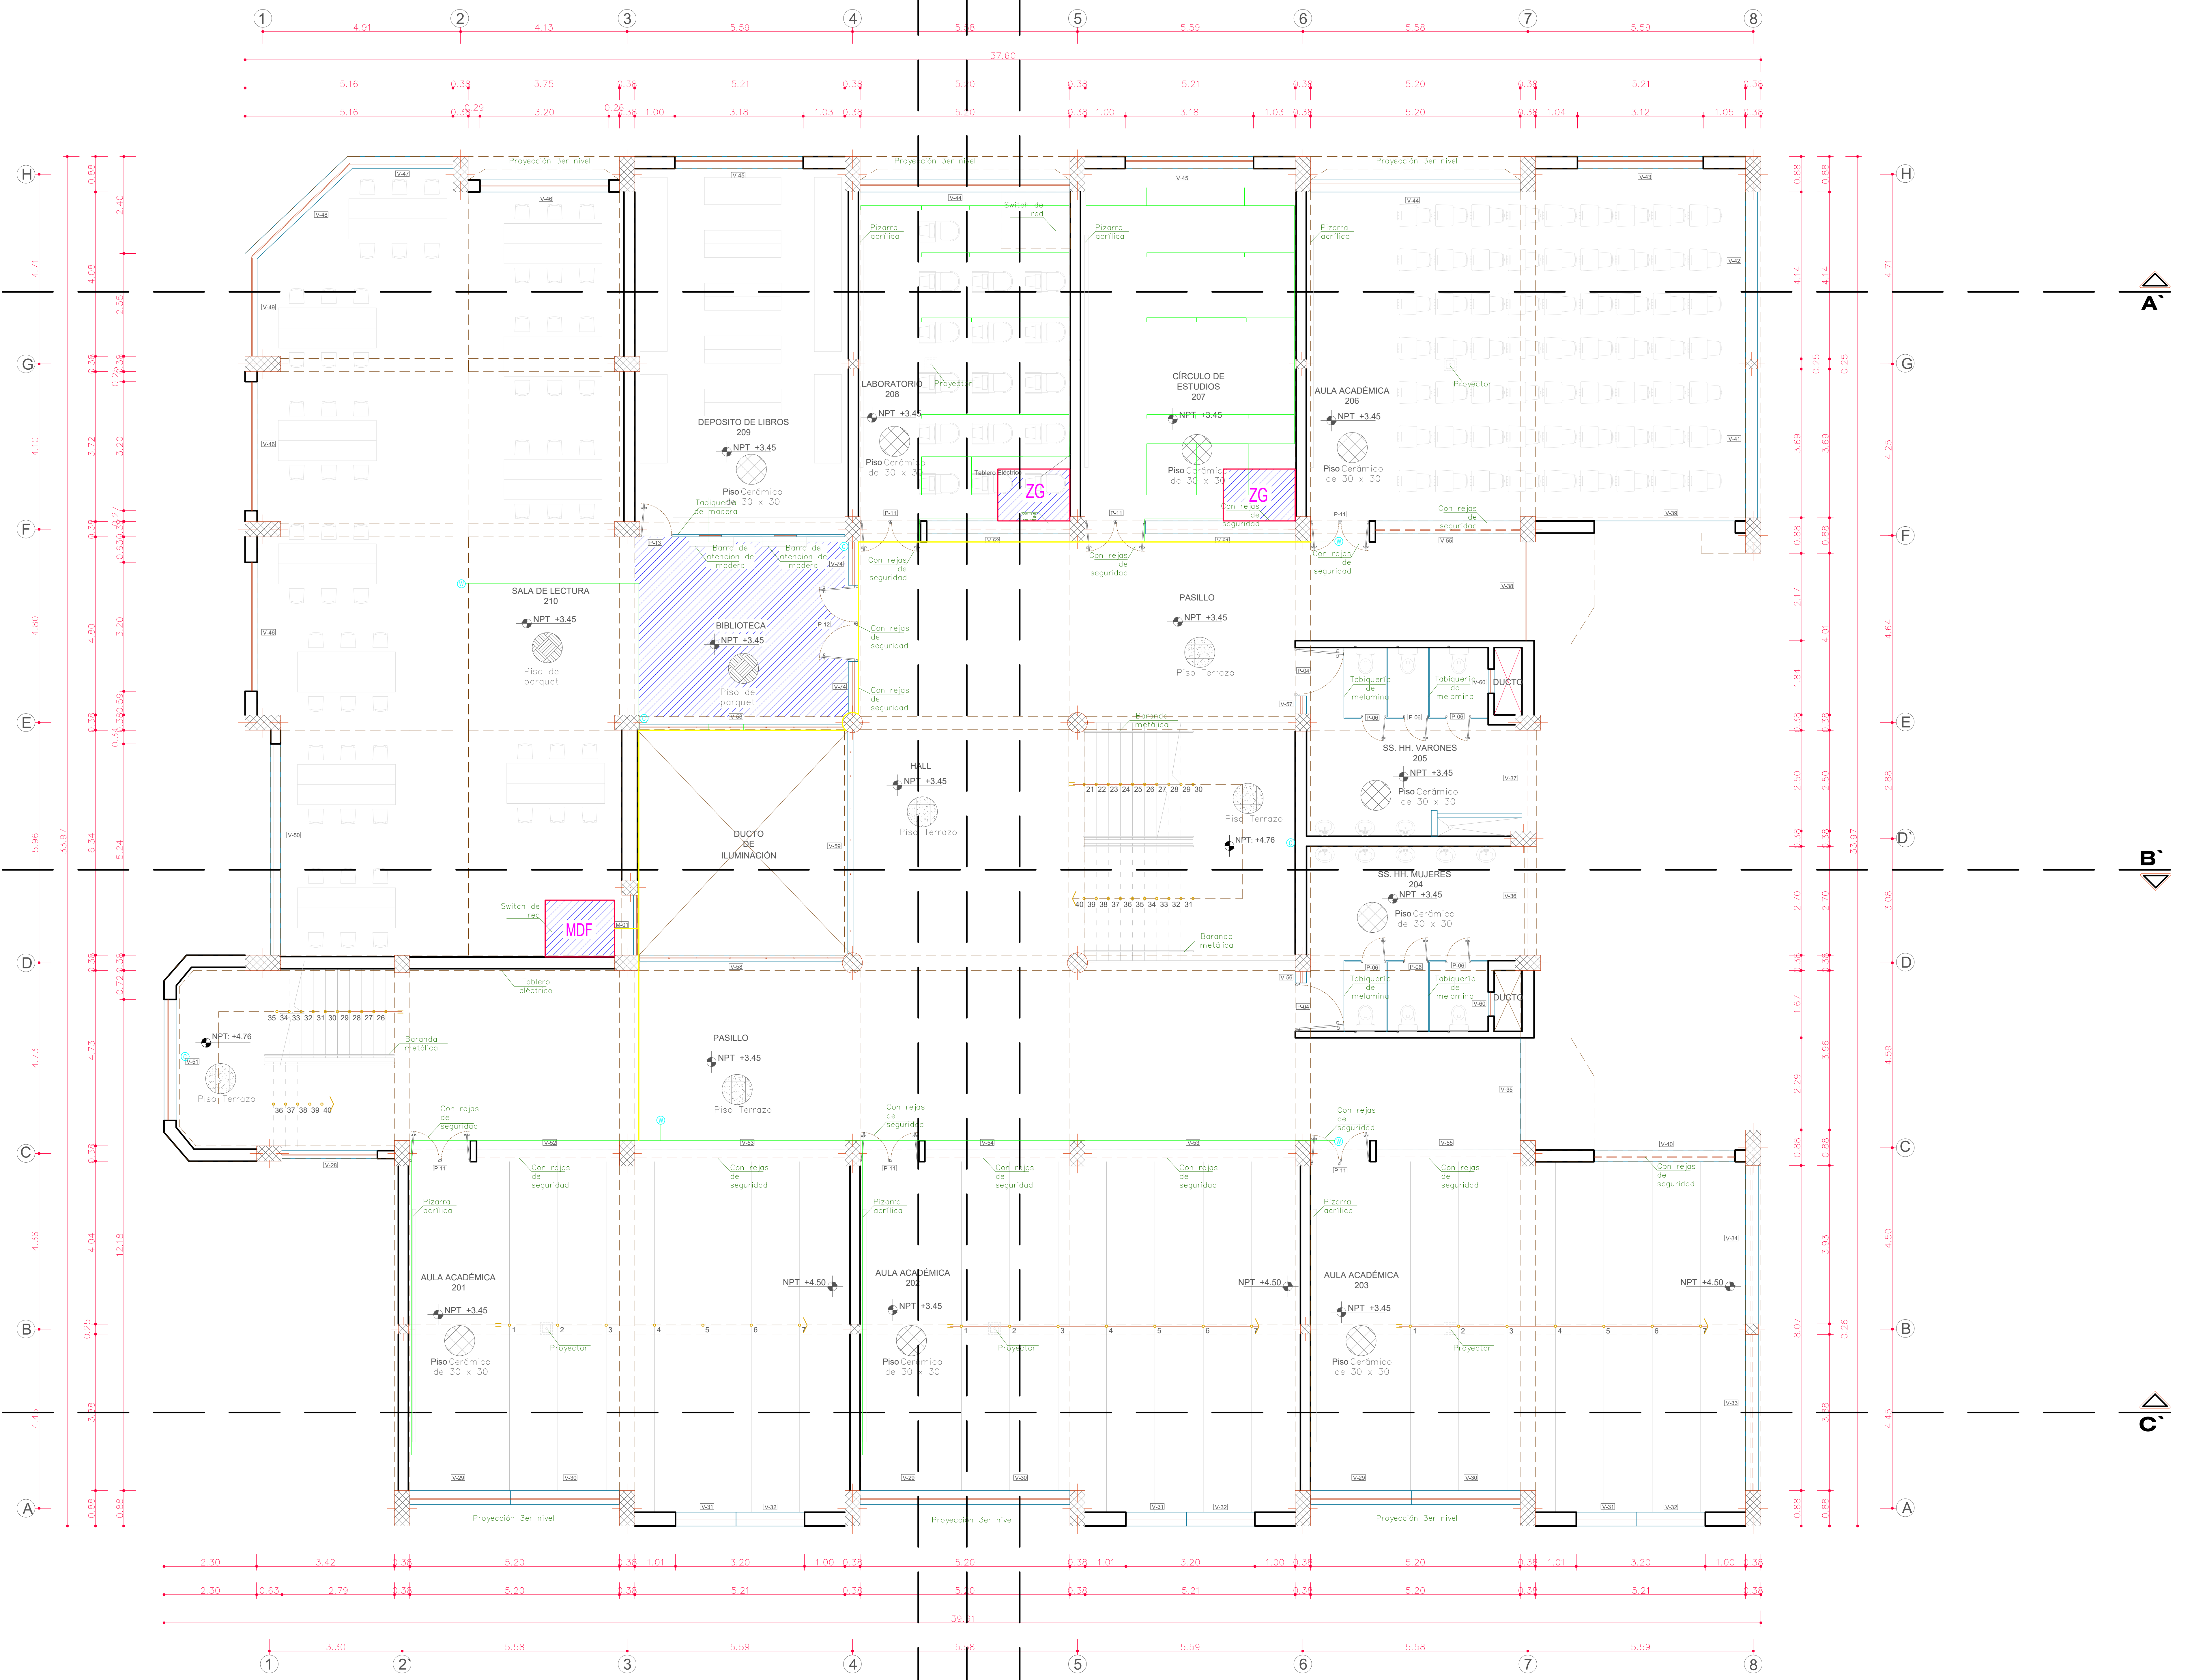

PLANO DE DISTRIBUCION SEGUNDO NIVEL

LEVANTAMIENTO TOPOGRÁFICO
INTEGRAL DEL ESTADO ACTUAL
A DETALLE DE LA
INFRAESTRUCTURA INTERIOR Y
EXTERIOR DE LA CIUDAD
UNIVERSITARIA

PABELLON PERAYOC-UNSAAC
09. INFORMATICA Y
SISTEMAS

PLANO

PLANO DE DISTRIBUCION
SEGUNDO NIVEL

ART. DE PROYECTO: JORGE SALCEDO QUISPE
 COORD. CAP: 5812
 ART. DE DISEÑO: AMED TEDILO MOSCOSO TOLEDO
 ART. DE DISEÑO: NELSON ROMANU SINCHI ROCA
 ART. DE DISEÑO: ANDRÉS DÍAZ CÁCERES
 ART. DE DISEÑO: ANDRÉS DELGADO
 ART. DE DISEÑO: ANDRÉS PAUCAR YEDA
 ART. DE DISEÑO: ANDRÉS CUSQUISPE QUISPE
 BOCH. ART. DE DISEÑO: DANDY BARRENTOS RAMOS
 BOCH. ART. DE DISEÑO: ADRIANA ANDRÉS ALDILLA
 BOCH. ART. DE DISEÑO: KENY CHOQUE INCAUTIPA
 ASIST. JHONATAN CASASVERDE COCUCCA

UBICACIÓN: CUSCO UNIVERSITARIA DE PERAYOC, CAMPA
 Distrito: CUSCO
 Provincia: CUSCO
 Departamento: CUSCO

ESCALA: INDICADAS
 FECHA: Cusco, Diciembre del 2019