


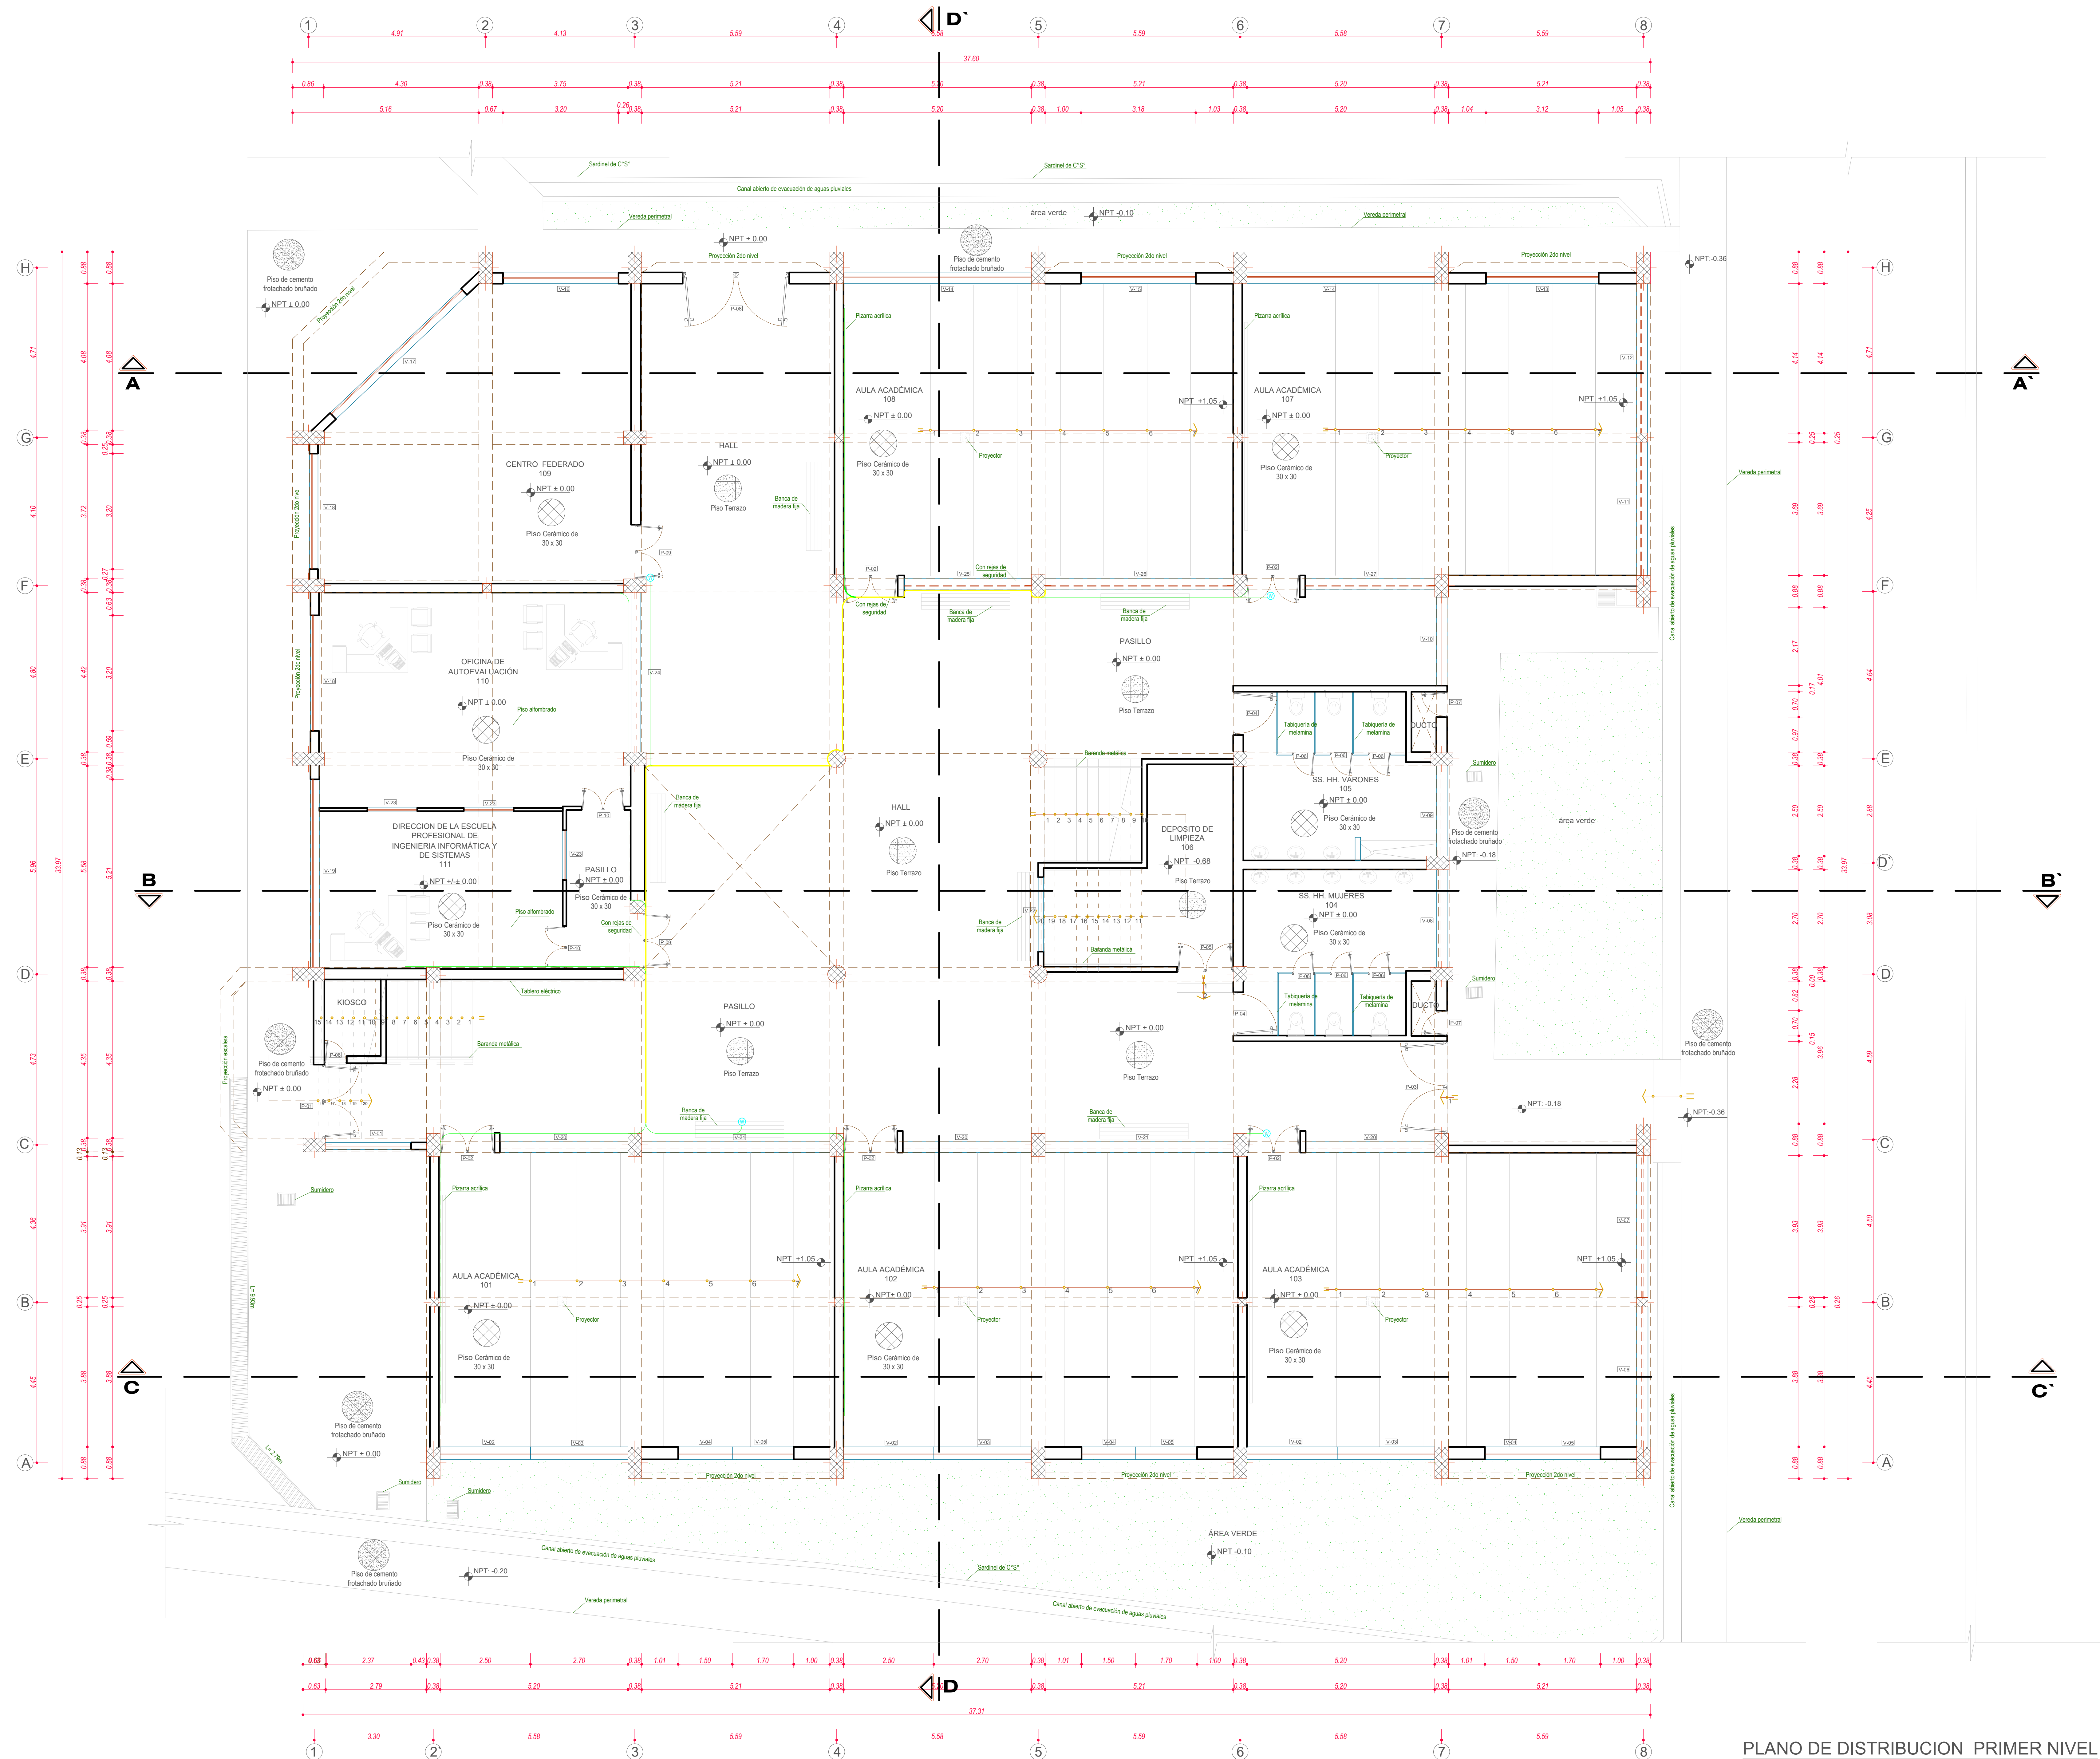

CUADRO DE VANOS			
CODIGO	ALFEIZER	ANCHO	ALTO
V-1	1.20	2.37	1.60
V-2	1.20	2.50	1.60
V-3	variable	2.70	1.60
V-4	variable	1.50	1.60
V-5	variable	1.70	1.60
V-6	1.80	3.88	0.75
V-7	1.80	3.93	0.75
V-8	1.30	2.70	1.30
V-9	1.22	2.50	1.38
V-10	0.90	2.17	1.70
V-11	1.80	3.69	0.75
V-12	1.85	4.14	0.75
V-13	variable	3.12	1.75
V-14	variable	5.20	1.75
V-15	variable	3.18	1.75
V-16	1.05	3.20	1.75
V-17	1.05	5.00	2.15
V-18	1.05	3.20	1.55
V-19	1.05	5.21	1.55
V-20	2.28	3.55	0.52
V-21	1.98	5.21	1.22
V-22	2.13	2.06	0.47
V-23	1.10	1.38	1.17
V-24	2.28	4.42	0.52
V-25	2.28	3.52	0.52
V-26	2.28	5.21	0.52
V-27	2.28	3.59	0.52

CUADRO DE VANOS		
CODIGO	ANCHO	ALTO
P-1	2.08	2.60
P-2	1.51	2.80
P-3	2.55	2.60
P-4	1.00	2.80
P-5	1.55	2.10
P-6	0.62	2.50
P-7	0.70	1.75
P-8	2.95	2.80
P-9	1.50	2.60
P-10	1.19	3.20

PLANO DE DISTRIBUCION PRIMER NIVEL
ESC:1/75



LEVANTAMIENTO TOPOGRÁFICO INTEGRAL
DEL ESTADO ACTUAL A DETALLE DE LA
INFRAESTRUCTURA INTERIOR Y EXTERIOR
DE LA CIUDAD UNIVERSITARIA DE
PERAYOC-UNSAAC

PARCELAS:
09. INFORMATICA Y SISTEMAS

PLANO:
PLANO DE DISTRIBUCION
PRIMER NIVEL

AREA DE PROYECTO		CAP. 3413
Arqº JORGE BALCEDO QUISPE		
EQUIPO TECNICO		
Arqº ARIEL TELLO MORALES TOLEDO	CAP. 13006	
Arqº MELBA COMAS SANCHEZ RODA	CAP. 13017	
Arqº SOLANGE DIAZ CACERES	CAP. 13016	
Arqº VILMA CUSI DELGADO	CAP. 13015	
Arqº JUAN CARLOS PALACIOS VEGA	CAP. 11059	
Bach. Arqº JANA GUSQUISE QUISPE		
Bach. Arqº DANY BARRIENTOS RAMOS		
Bach. Arqº ROSANA AGUIRRE AGUIRRE		
Bach. Arqº KENY CHOCQUE INCAUTIPRA		
Asst. JONATAN CASAHUARE COCORA		

UBICACION		LAMINA
Distrito	CUSCO	P-09
Provincia	CUSCO	AR - 01
Departamento	CUSCO	
FECHA		INDICADAS
Cusco, Diciembre del 2016		