


CUADRO DE VANOS					
CODIGO	ALFEIZER	ANCHO	ALTO	CODIGO	ANCHO
V-29	0.80	2.50	1.60	P-4	1.00
V-30	variable	2.70	1.60	P-6	0.82
V-31	variable	1.50	1.60	P-11	1.51
V-32	variable	1.70	1.60	P-14	1.89
V-36	1.26	2.70	0.99	P-15	0.90
V-37	1.26	2.50	0.99	P-16	0.95
V-39	1.68	3.50	0.72	P-17	0.80
V-41	1.85	3.69	0.75	P-18	1.50
V-42	1.50	4.14	0.75	M-1	1.49
V-43	0.80	3.12	1.60	M-3	4.16
V-44	0.80	5.20	1.60		
V-45	0.80	3.18	1.60		
V-46	0.80	3.20	1.60		
V-47	0.80	2.62	1.60		
V-48	0.80	3.50	1.60		
V-49	0.80	2.55	1.60		
V-50	0.80	5.24	1.60		
V-55	0.45	0.30	1.80		
V-57	0.45	0.45	1.80		
V-58	0.44	5.03	1.96		
V-59	0.44	5.46	1.81		
V-60	1.00	0.60	1.40		
V-62	0.40	2.37	1.60		
V-63	1.05	3.88	0.75		
V-64	1.05	3.93	0.75		
V-65	variable	3.48	0.75		
V-66	1.00	3.00	1.96		
V-67	1.90	3.55	0.50		
V-68	1.90	3.59	0.50		
V-69	1.90	3.60	0.50		
V-70	1.90	3.58	0.50		
V-71	1.66	3.70	0.74		
V-72	0.95	1.75	1.30		
V-73	1.00	0.80	1.30		

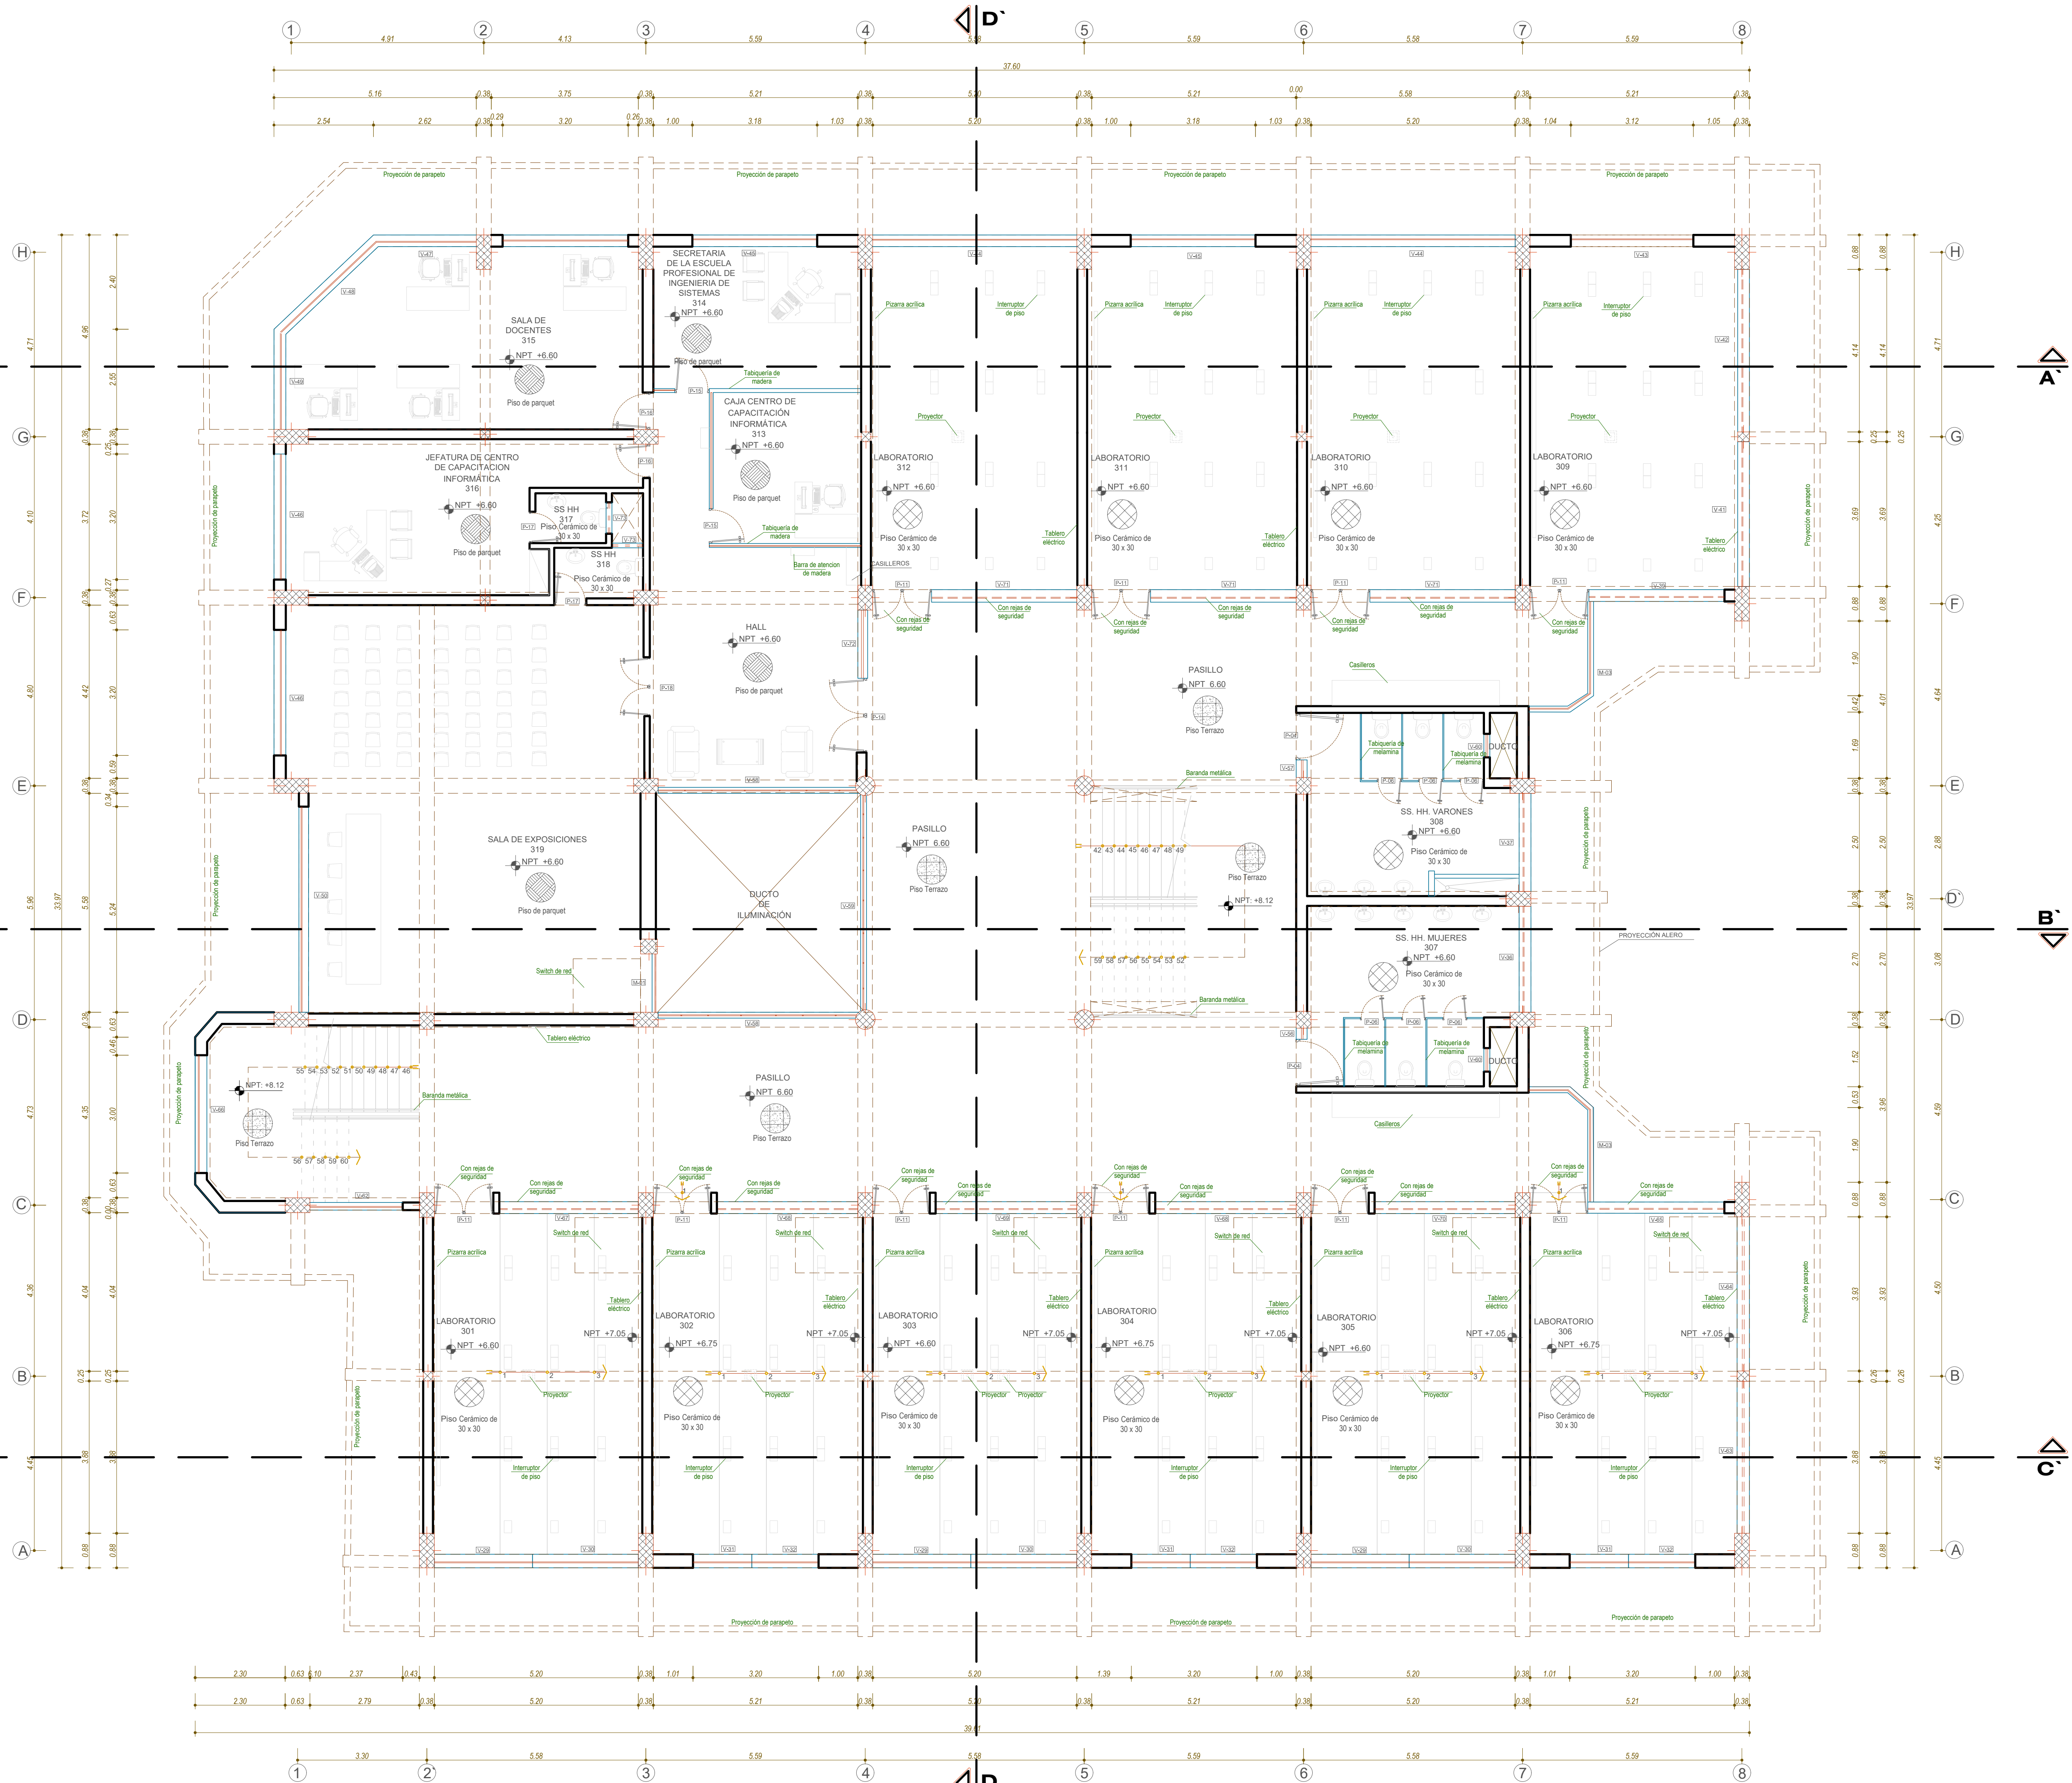

PLANO DE DISTRIBUCION TERCER NIVEL
ESC:1/75



LEVANTAMIENTO TOPOGRAFICO INTEGRAL
DEL ESTADO ACTUAL A DETALLE DE LA
INFRAESTRUCTURA INTERIOR Y EXTERIOR
DE LA CIUDAD UNIVERSITARIA DE
PERAYOC-UNSC

PROYECTO
09. INFORMATICA Y SISTEMAS

PLANO
PLANO DE DISTRIBUCION
TERCER NIVEL

LISTA DE PROYECTOS	
Ases. Jorge Salcedo Quirope	CAP. 1812
LISTA DE REVISIONES	
Ases. Arnel Toledo Moscoso Toledo	CAP. 1300
Ases. Milda Concha Banchi Banchi	CAP. 1817
Ases. Solange Diaz Caceres	CAP. 1816
Ases. Vilma Cruz Delgado	CAP. 1815
Ases. Juan Carlos Páucar Vega	CAP. 1155
Ases. Anna Coussepe Quirope	
Ases. Andy Barrientos Ramos	
Ases. Adriana Acuña Acuña	
Ases. Kery Choque Incaoutpa	
Ases. Jonathan Casavieje Cordera	

INDICACIONES	
COORDINADAS DE PERAYOC	
Dirección	USC
Provincia	USC
Departamento	USC
INDICACIONES	
FECHA	2019
INDICACIONES	

P-09
AR - 03