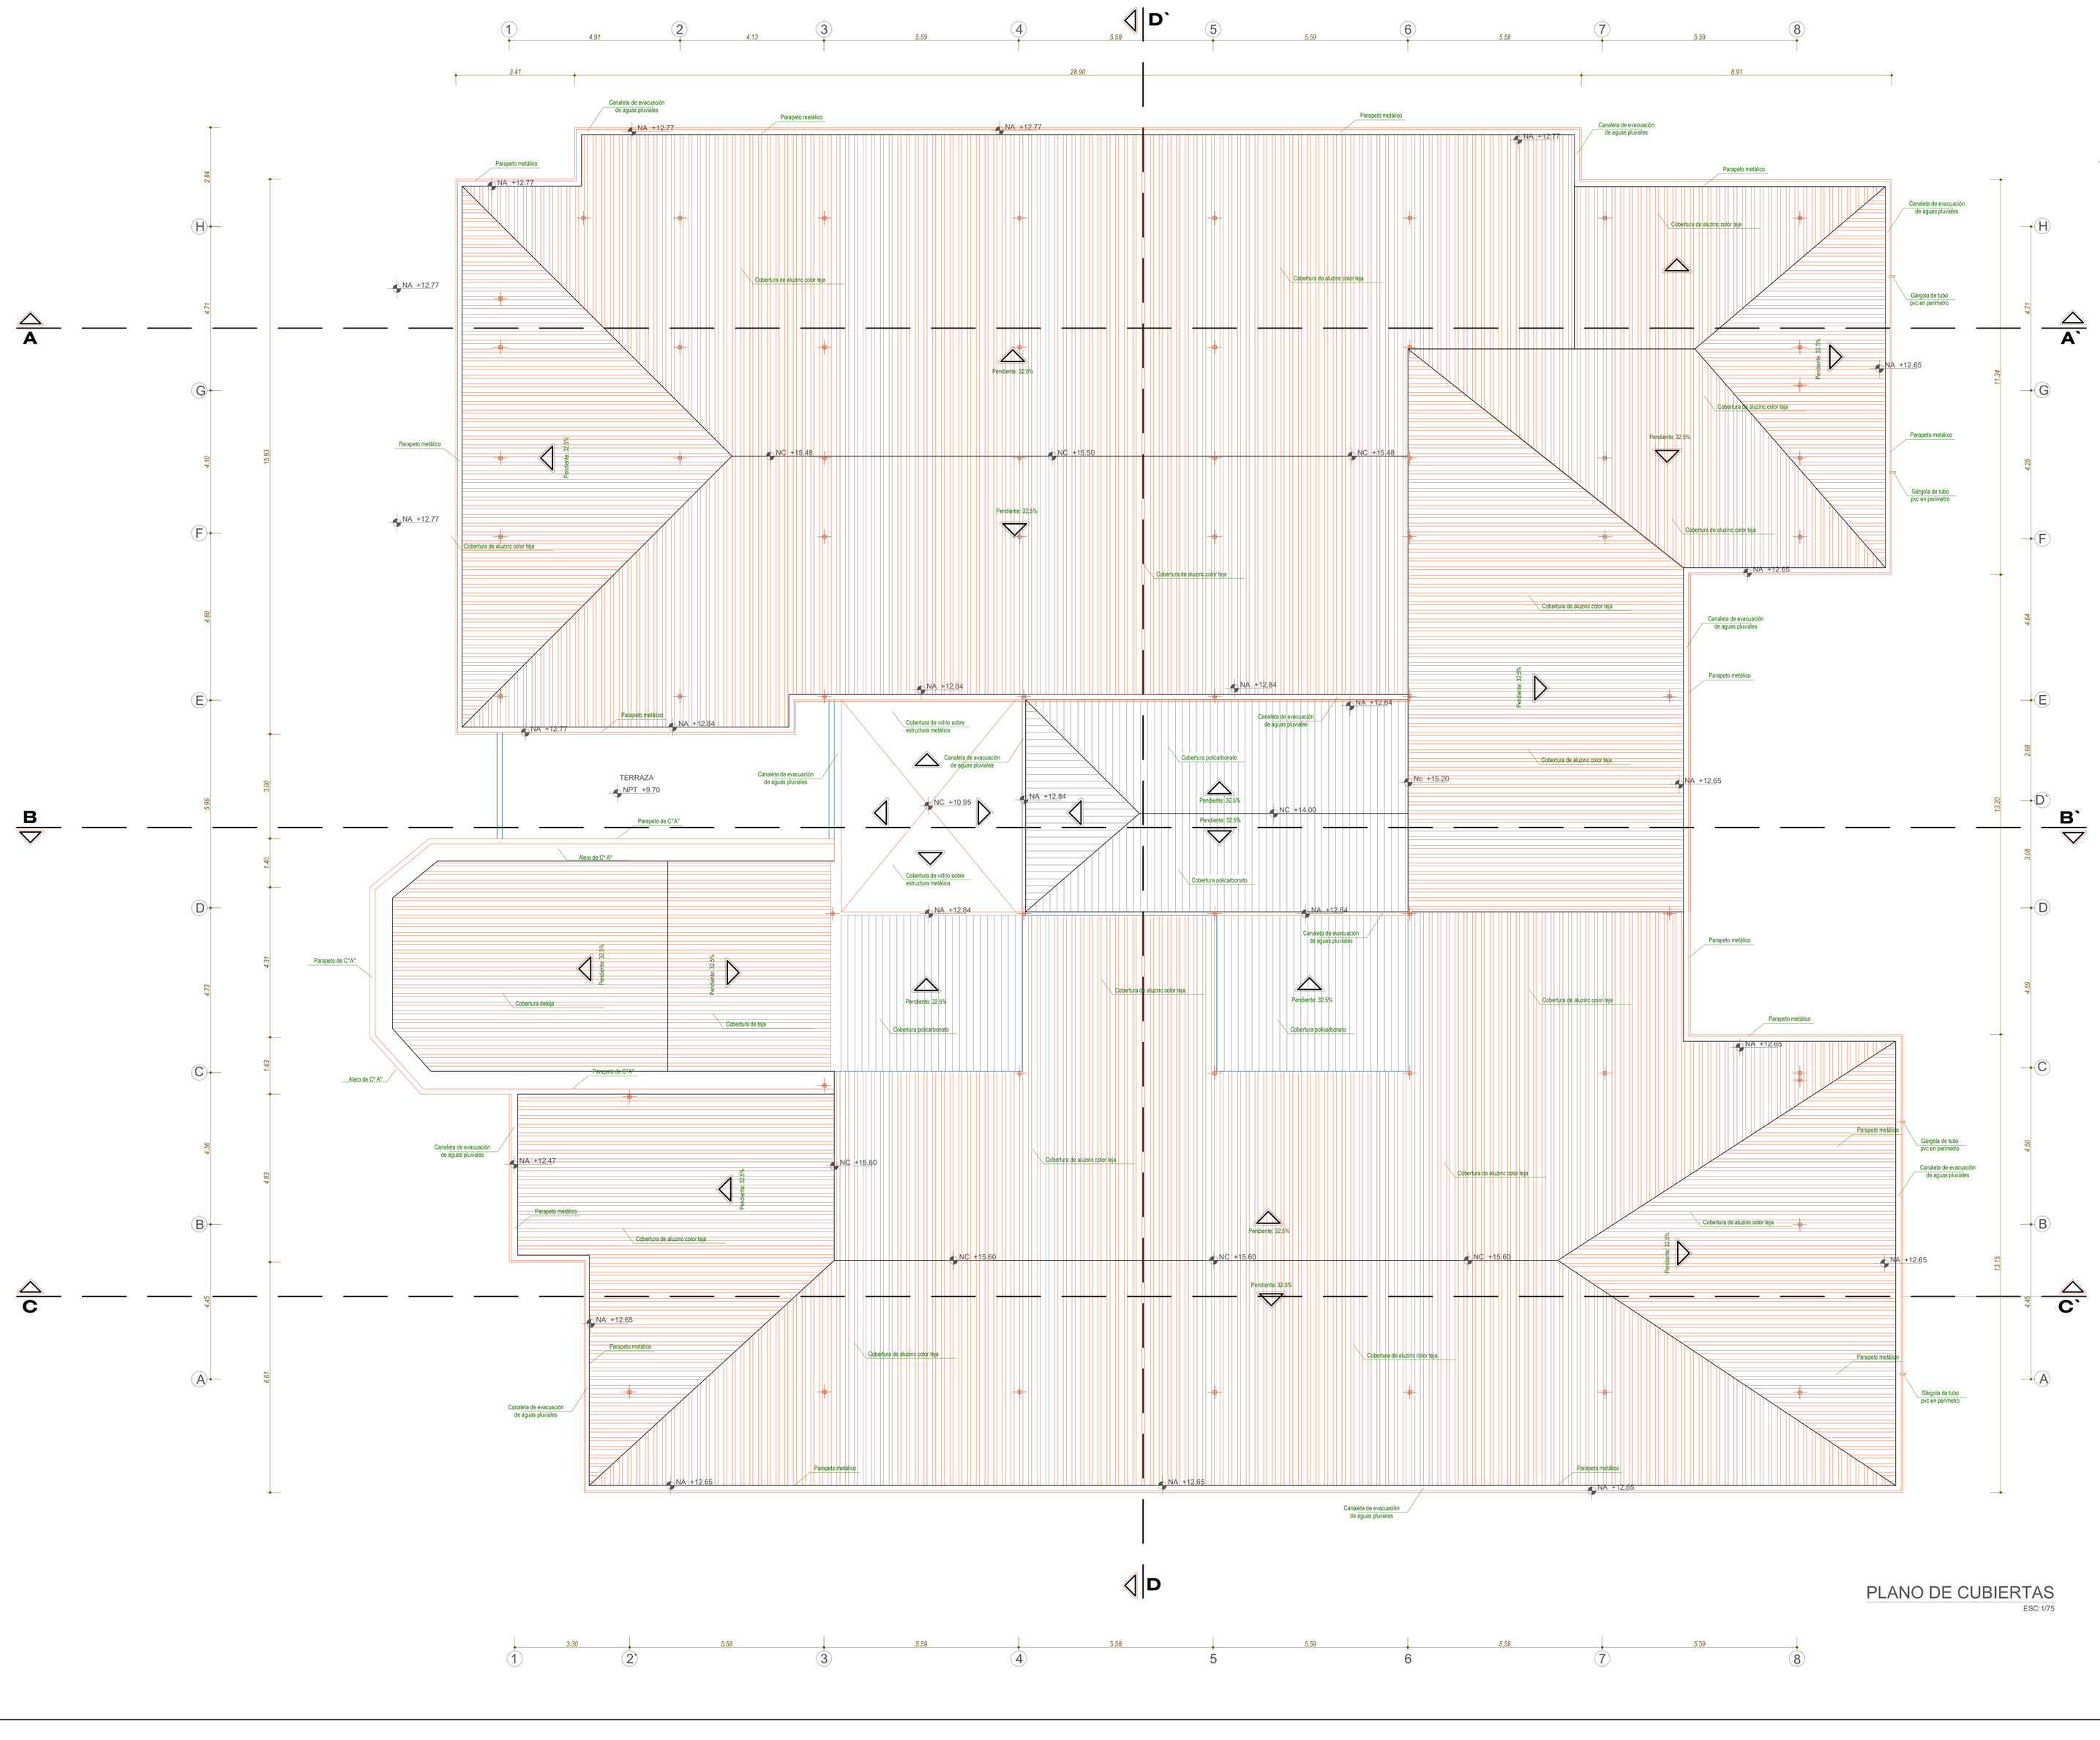

Gremsa
CONSULTORIA - OBRAS INTERVENCIONES

LEVANTAMIENTO TOPOGRÁFICO INTEGRAL DEL ESTADO ACTUAL A DETALLE DE LA INFRAESTRUCTURA INTERIOR Y EXTERIOR DE LA CIUDAD UNIVERSITARIA DE PERAYOC-UNSAAC

PABELLON:
09. INFORMATICA Y SISTEMAS

PLANO:
PLANO DE CUBIERTAS

JEFE DE PROYECTO:
Arqto° JORGE SALCEDO QUISPE — CAP 5812

EQUIPO TECNICO:
Arqto° AMEO TEODLIO MOSCOSO TOLEDO — CAP 13006
Arqta° NÉLIDA COANQUI SINCHI ROCA — CAP 12517
Arqta° SOLANGE DIAZ CACERES — CAP 12616
Arqta° VILMA CLISI DELGADO — CAP 12615
Arqto° JUAN CARLOS PAUCAR VEGA — CAP 11059
Bach. Arqta° JANIA CUSIQUISPE QUISPE
Bach. Arqto° DANDY BARRIENTOS RAMOS
Bach. Arqta° ADRIANA AIQUIPA ALOSILLA
Bach. Arqto° KENY CHOQUE INCACUTIPA
Aseje. JHONATAN CASAVERDE CCOICCA

UBICACION:
CIUDAD UNIVERSITARIA DE PERAYOC
Distrito : CUSCO
Provincia : CUSCO
Departamento : CUSCO

ESCALA:
INDICADAS

FECHA:
Cusco, Diciembre del 2016

LAMINA:
P-09
AR - 05

PLANO DE CUBIERTAS
ESC: 1/75