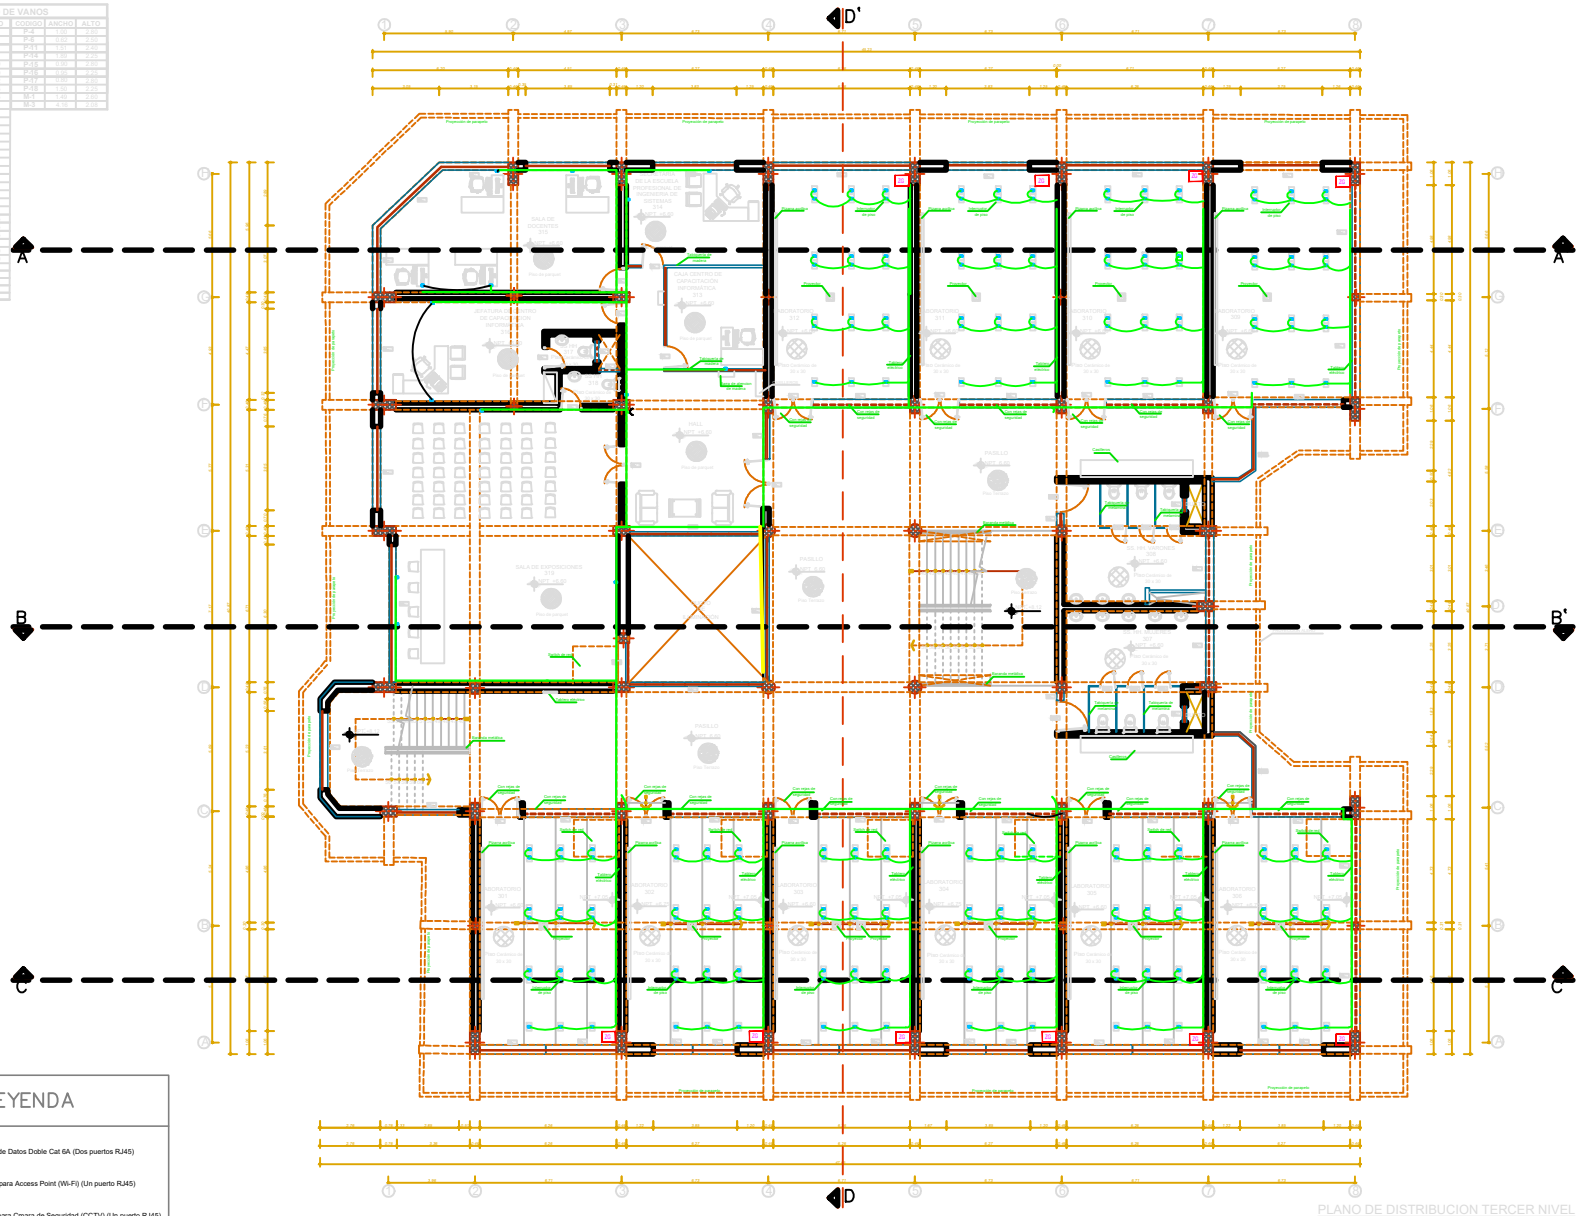


LEYENDA

- Toma de Datos Doble Cat 6A (Dos puertos RJ45)
- Punto para Access Point (Wi-Fi) (Un puerto RJ45)
- Punto para Cmara de Seguridad (CCTV) (Un puerto RJ45)

LEVANTAMIENTO TOPOGRÁFICO INTEGRAL DEL ESTADO ACTUAL A DETALLE DE LA INFRAESTRUCTURA INTERIOR Y EXTERIOR DE LA CIUDAD UNIVERSITARIA DE PERAYOC-UNSAAC

09. INFORMATICA Y SISTEMAS

PLANO DE DISTRIBUCION TERCER NIVEL

P-09

AR- 03

PLANO DE DISTRIBUCION TERCER NIVEL

Created in Free Online PDF to DWG Converter by CADSoftTools
http://www.cadsofttools.com/pdf-to-dwg-online/