CUADRO DE VANOS

CODIGO	ALFEIZER	ANCHO	ALTO
V-75	1.20	1.34	variable
V-76	1.20	0.78	variable
V-77	1.20	1.40	1.67
V-78	1.20	2.04	1.67
V-79	1.20	2.26	1.67
V-80	1.20	2.24	1.67
V-81	1.20	2.25	1.67
V-82	1.20	3.30	1.67
V-83	1.20	1.20	1.67
V-84	0.31	2.40	2.56
V-85	0.72	4.25	2.15
V-86	0.31	3.20	2.56
V-87	0.72	5.50	2.15
V-88	0.72	3.62	2.15
V-89	1.20	3.20	1.67
V-90	1.95	1.60	0.92
V-91	1.72	1.62	1.00
V-92	1.69	0.77	0.90
V-93	1.70	0.77	1.99
V-94	1.72	1.62	1.00
V-95	1.69	1.62	0.89
V-96	1.69	1.63	0.89
V-97	0.31	2.66	2.56
V-98	0.31	3.33	2.56
V-99	0.31	1.29	2.56
V-100	0.31	1.99	2.56
V-101	0.31	2.16	2.56
V-102	0.31	3.19	2.56
V-103	0.31	2.74	2.56
V-104	1.20	4.33	1.67
V-105	1.20	5.80	1.67
V-106	1.75	5.50	1.67
V-107	0.70	5.67	2.17
V-108	0.70	6.14	2.17

CODIGO	ANCHO	ALTO
P-19	1.00	2.80
P-20	2.40	2.87
P-21	1.00	2.15
P-22	1.00	2.10
P-23	1.62	2.80
M-2	2.02	2.87

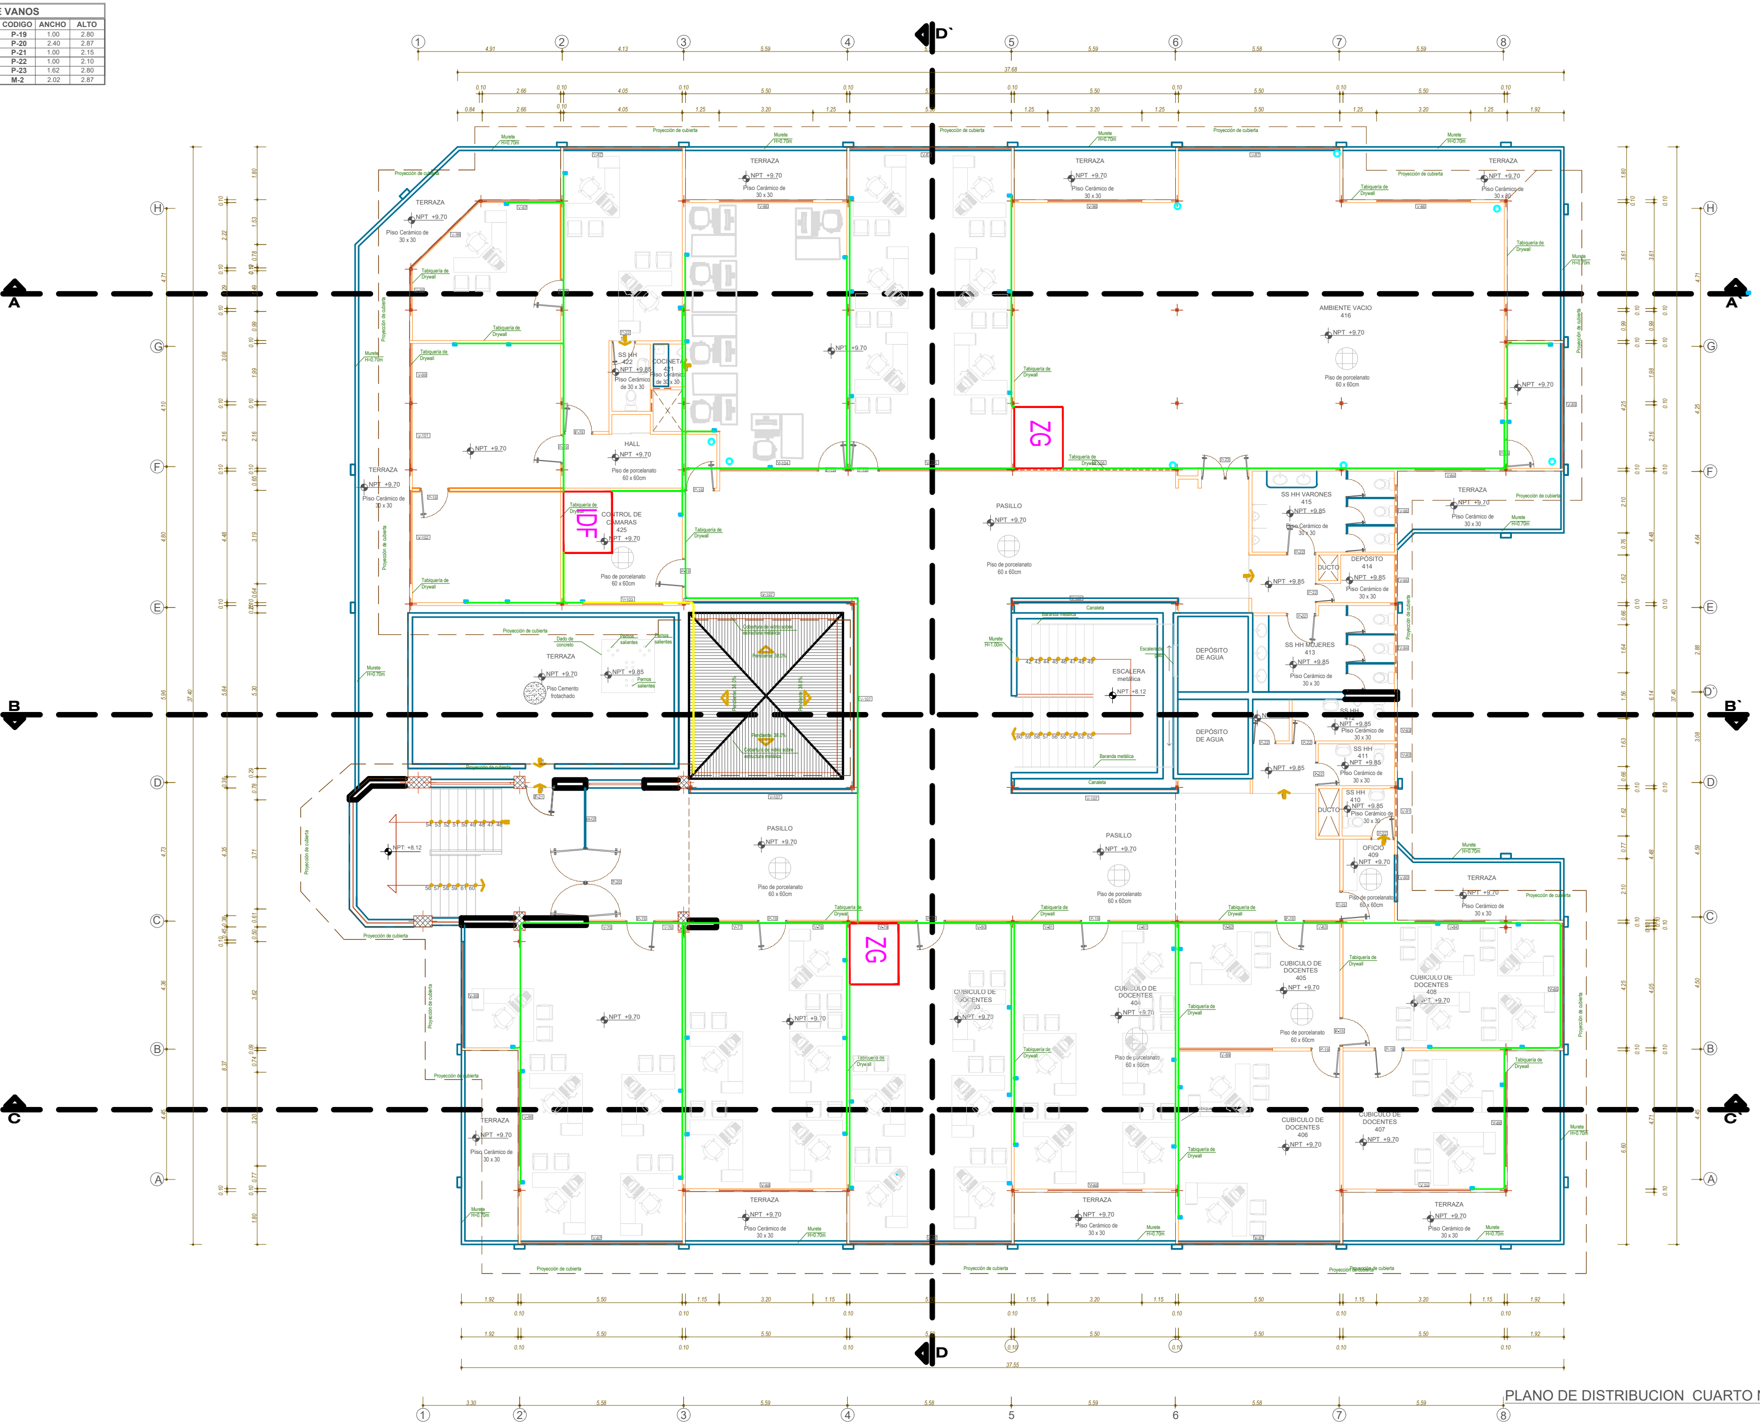

PLANO DE DISTRIBUCION CUARTO NIVEL
ESC:1/75

Gremsa
CONSULTORIA - OBRAS
INVERSIONES

LEVANTAMIENTO TOPOGRÁFICO INTEGRAL
DEL ESTADO ACTUAL A DETALLE DE LA
INFRAESTRUCTURA INTERIOR Y EXTERIOR
DE LA CIUDAD UNIVERSITARIA DE
PERAYOC-UNSAAC

PABELLON:
09. INFORMATICA Y SISTEMAS

PLANO:
PLANO DE DISTRIBUCION
CUARTO NIVEL

JEFE DE PROYECTO:
Arqto° JORGE SALCEDO QUISPE CAP 5812

EQUIPO TÉCNICO:
Arqto° AMED TEDILIO MOSCOSO TOLEDO CAP 13006
Arqta° NÉLIDA COANQUI SINCHI ROCA CAP 12517
Arqta° SOLANGE DIAZ CACERES CAP 12616
Arqta° VILMA CUSI DELGADO CAP 12615
Arqto° JUAN CARLOS PAUCAR VEGA CAP 11059
Bach. Arqta° JANIA CUSIQUISPE QUISPE
Bach. Arqto° DANDY BARRIENTOS RAMOS
Bach. Arqta° ADRIANA AIQUIPA ALOSILLA
Bach. Arqto° KENY CHOQUE INCACUTIPA
Asist. JHONATAN CASAVERDE CCOICCA

UBICACION:
CIUDAD UNIVERSITARIA DE PERAYOC
Distrito : CUSCO
Provincia : CUSCO
Departamento : CUSCO

ESCALA:
INDICADAS

FECHA:
Cusco, Diciembre del 2016

LAMINA:
P-09
AR - 04