


CUADRO DE VANOS					
CODIGO	ALFEIZER	ANCHO	ALTO	CODIGO	ANCHO
V-75	1.20	1.34	variable	P-19	1.00
V-76	1.20	0.78	variable	P-20	2.40
V-77	1.20	1.40	1.67	P-21	1.00
V-78	1.20	2.04	1.67	P-22	1.00
V-79	1.20	2.26	1.67	P-23	1.62
V-80	1.20	2.24	1.67	M-2	2.02
V-81	1.20	2.25	1.67		
V-82	1.20	3.30	1.67		
V-83	1.20	1.20	1.67		
V-84	0.31	2.40	2.56		
V-85	0.72	4.25	2.15		
V-86	0.31	3.20	2.56		
V-87	0.72	5.50	2.15		
V-88	0.72	3.62	2.15		
V-89	1.20	3.20	1.67		
V-90	1.95	1.60	0.92		
V-91	1.72	1.62	1.00		
V-92	1.69	0.77	0.90		
V-93	1.70	0.77	1.99		
V-94	1.72	1.62	1.00		
V-95	1.69	1.62	0.89		
V-96	1.69	1.63	0.89		
V-97	0.31	2.66	2.56		
V-98	0.31	3.33	2.56		
V-99	0.31	1.29	2.56		
V-100	0.31	1.99	2.56		
V-101	0.31	2.16	2.56		
V-102	0.31	3.19	2.56		
V-103	0.31	2.74	2.56		
V-104	1.20	4.33	1.67		
V-105	1.20	5.80	1.67		
V-106	1.75	5.50	1.67		
V-107	0.70	5.87	2.17		
V-108	0.70	6.14	2.17		

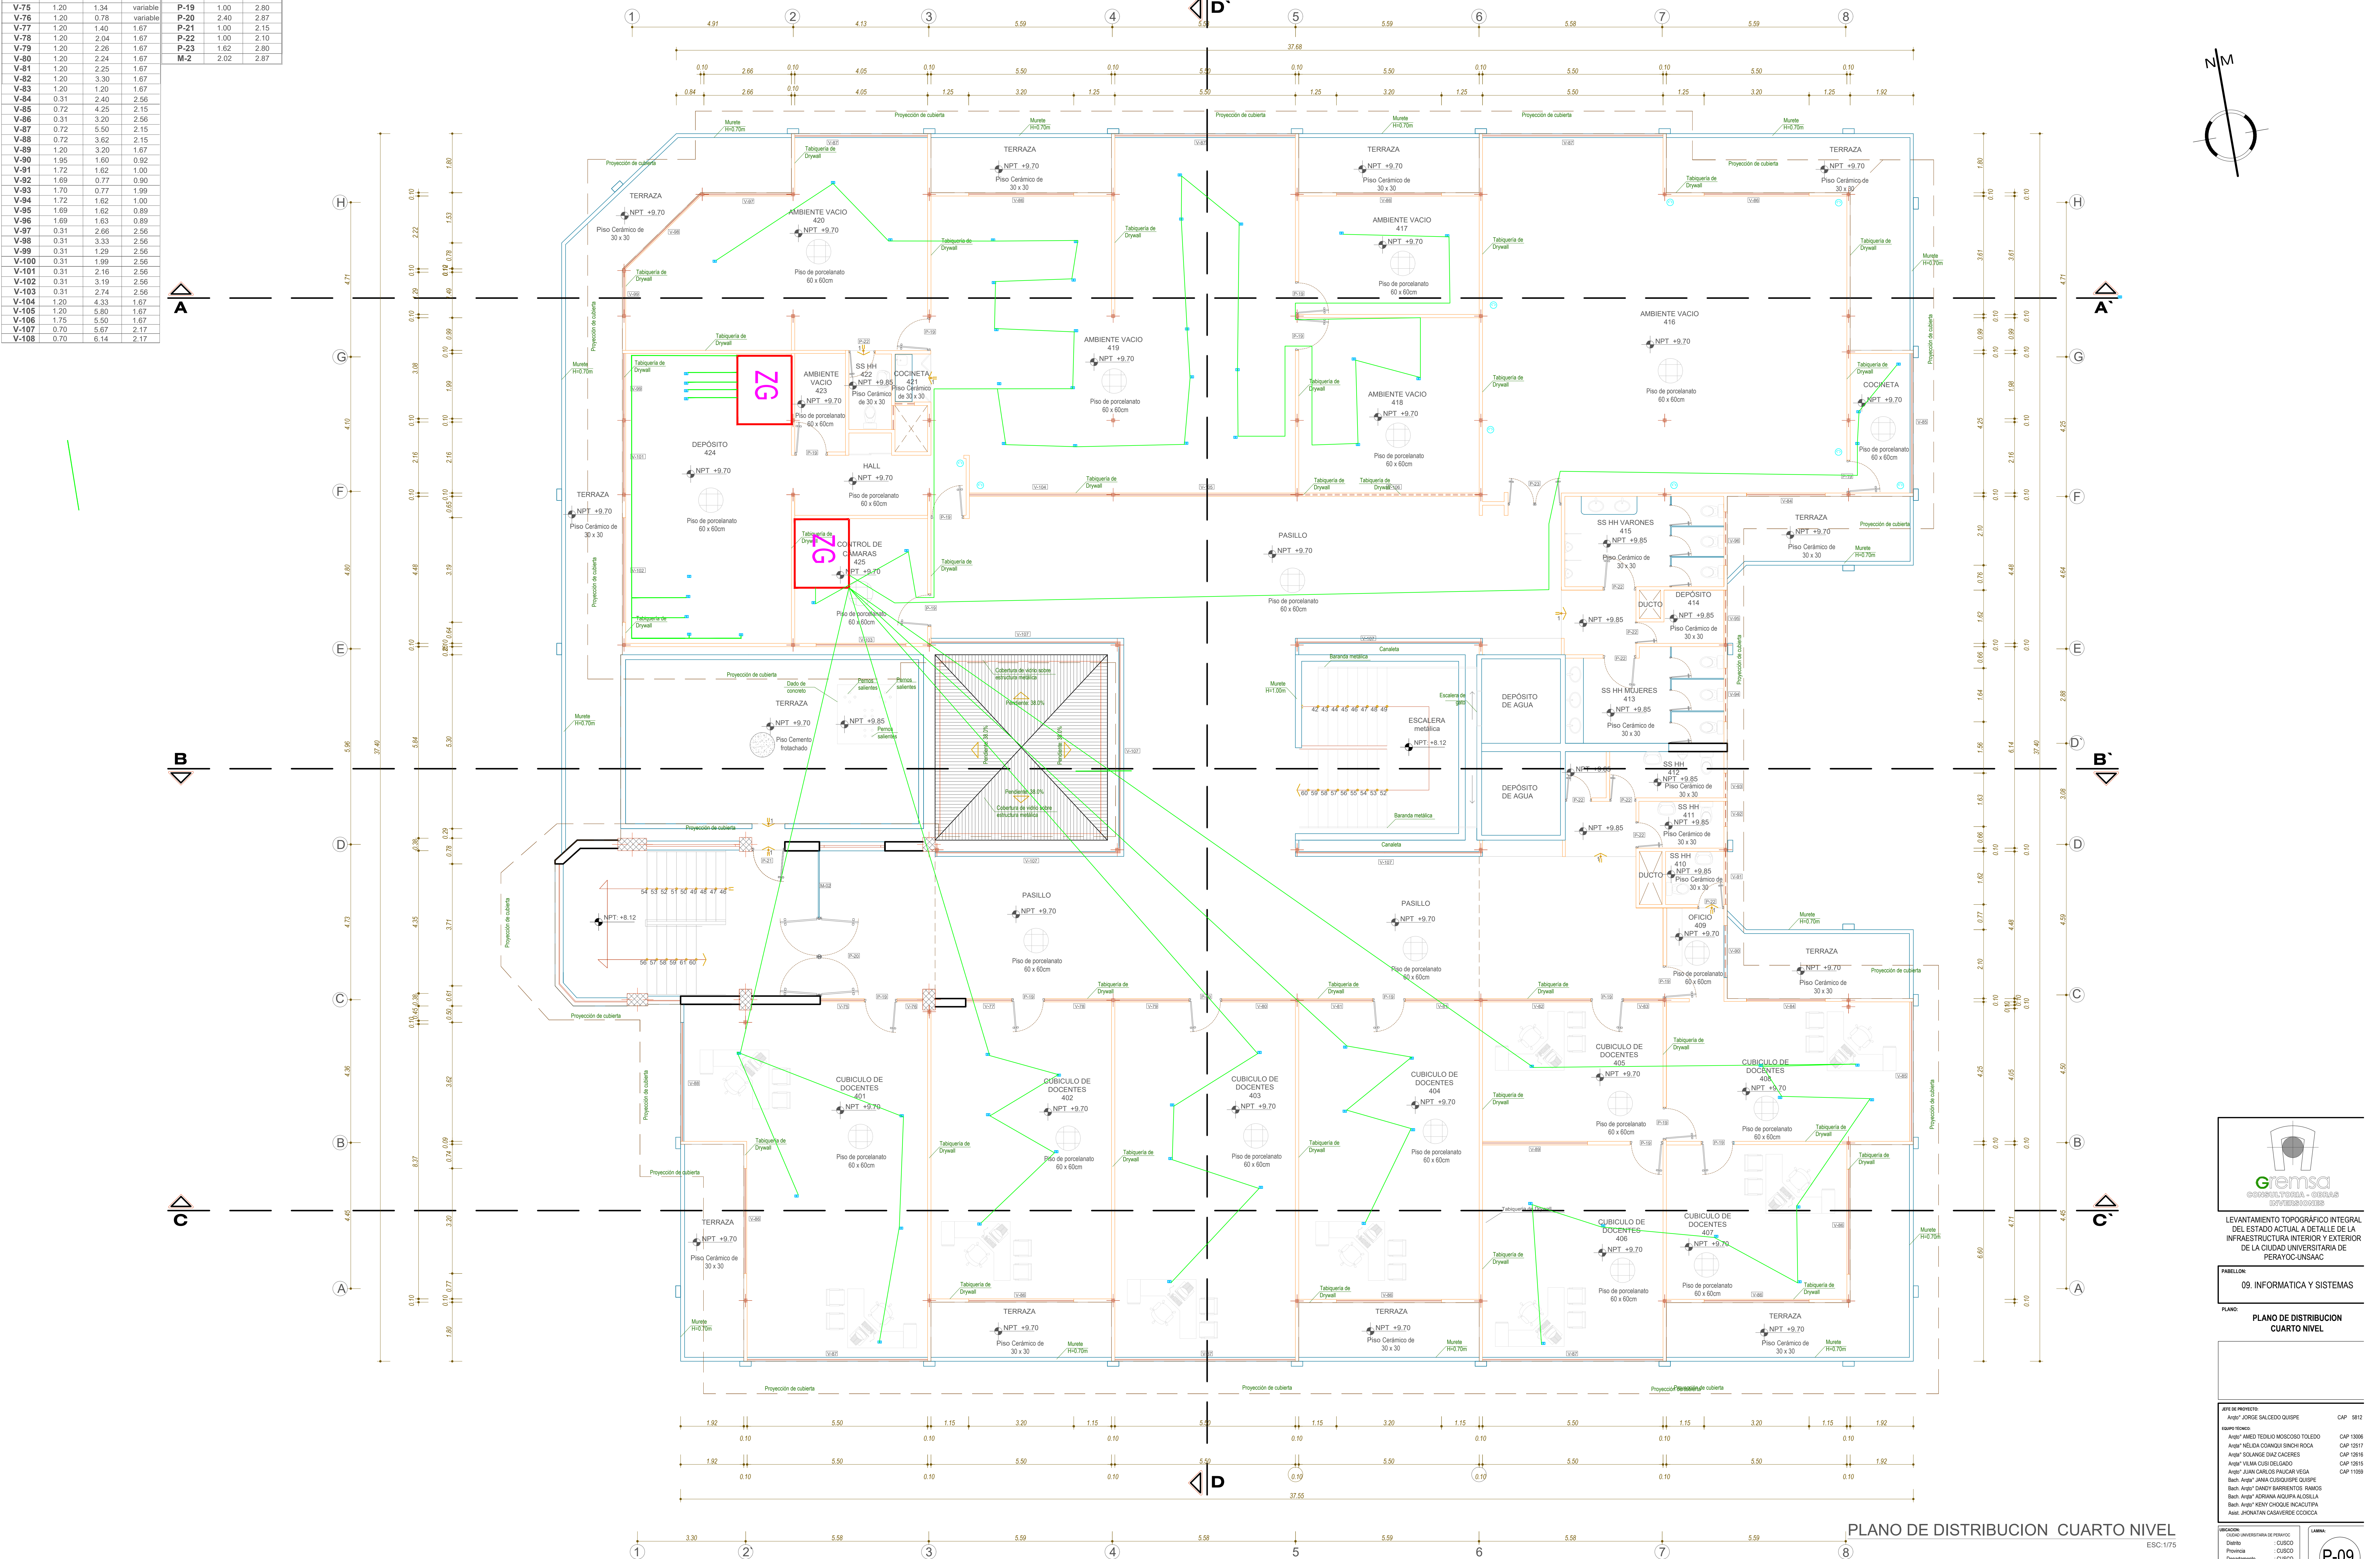

PLANO DE DISTRIBUCION CUARTO NIVEL

ESC: 1/75



Gremsa
CONSULTORES - OBRAS
CIVILES

LEVANTAMIENTO TOPOGRAFICO INTEGRAL
DEL ESTADO ACTUAL A DETALLE DE LA
INFRAESTRUCTURA INTERIOR Y EXTERIOR
DE LA CIUDAD UNIVERSITARIA DE
PERAYOC-UNSAAC

PAPELON:
09. INFORMATICA Y SISTEMAS

PLANO:
PLANO DE DISTRIBUCION
CUARTO NIVEL

Jefe de Proyecto:
Arq^a JORGE SALCEDO QUISEP

Arq^a JORGE SALCEDO QUISEP CAP 5812

Arq^a AMED TEDILO MOSCOSO TOLEDO CAP 13006

Arq^a NELDA GONZALEZ SANCHEZ ROCA CAP 12517

Arq^a SOLANGE DIAZ CASERES CAP 12816

Arq^a YILMA CUSI DELGADO CAP 12815

Arq^a JUAN CARLOS PAUCAR VEGA CAP 11059

Ing^a JHONATAN CASAVIERE COCCOA

UBICACION:
CIUDAD UNIVERSITARIA DE PERAYOC
Distrito: CUSCO
Provincia: CUSCO
Departamento: CUSCO

ESCALA:
INDICADAS

FECHA:
Cusco, Diciembre del 2016

LABOR:
P-09

AR - 04